




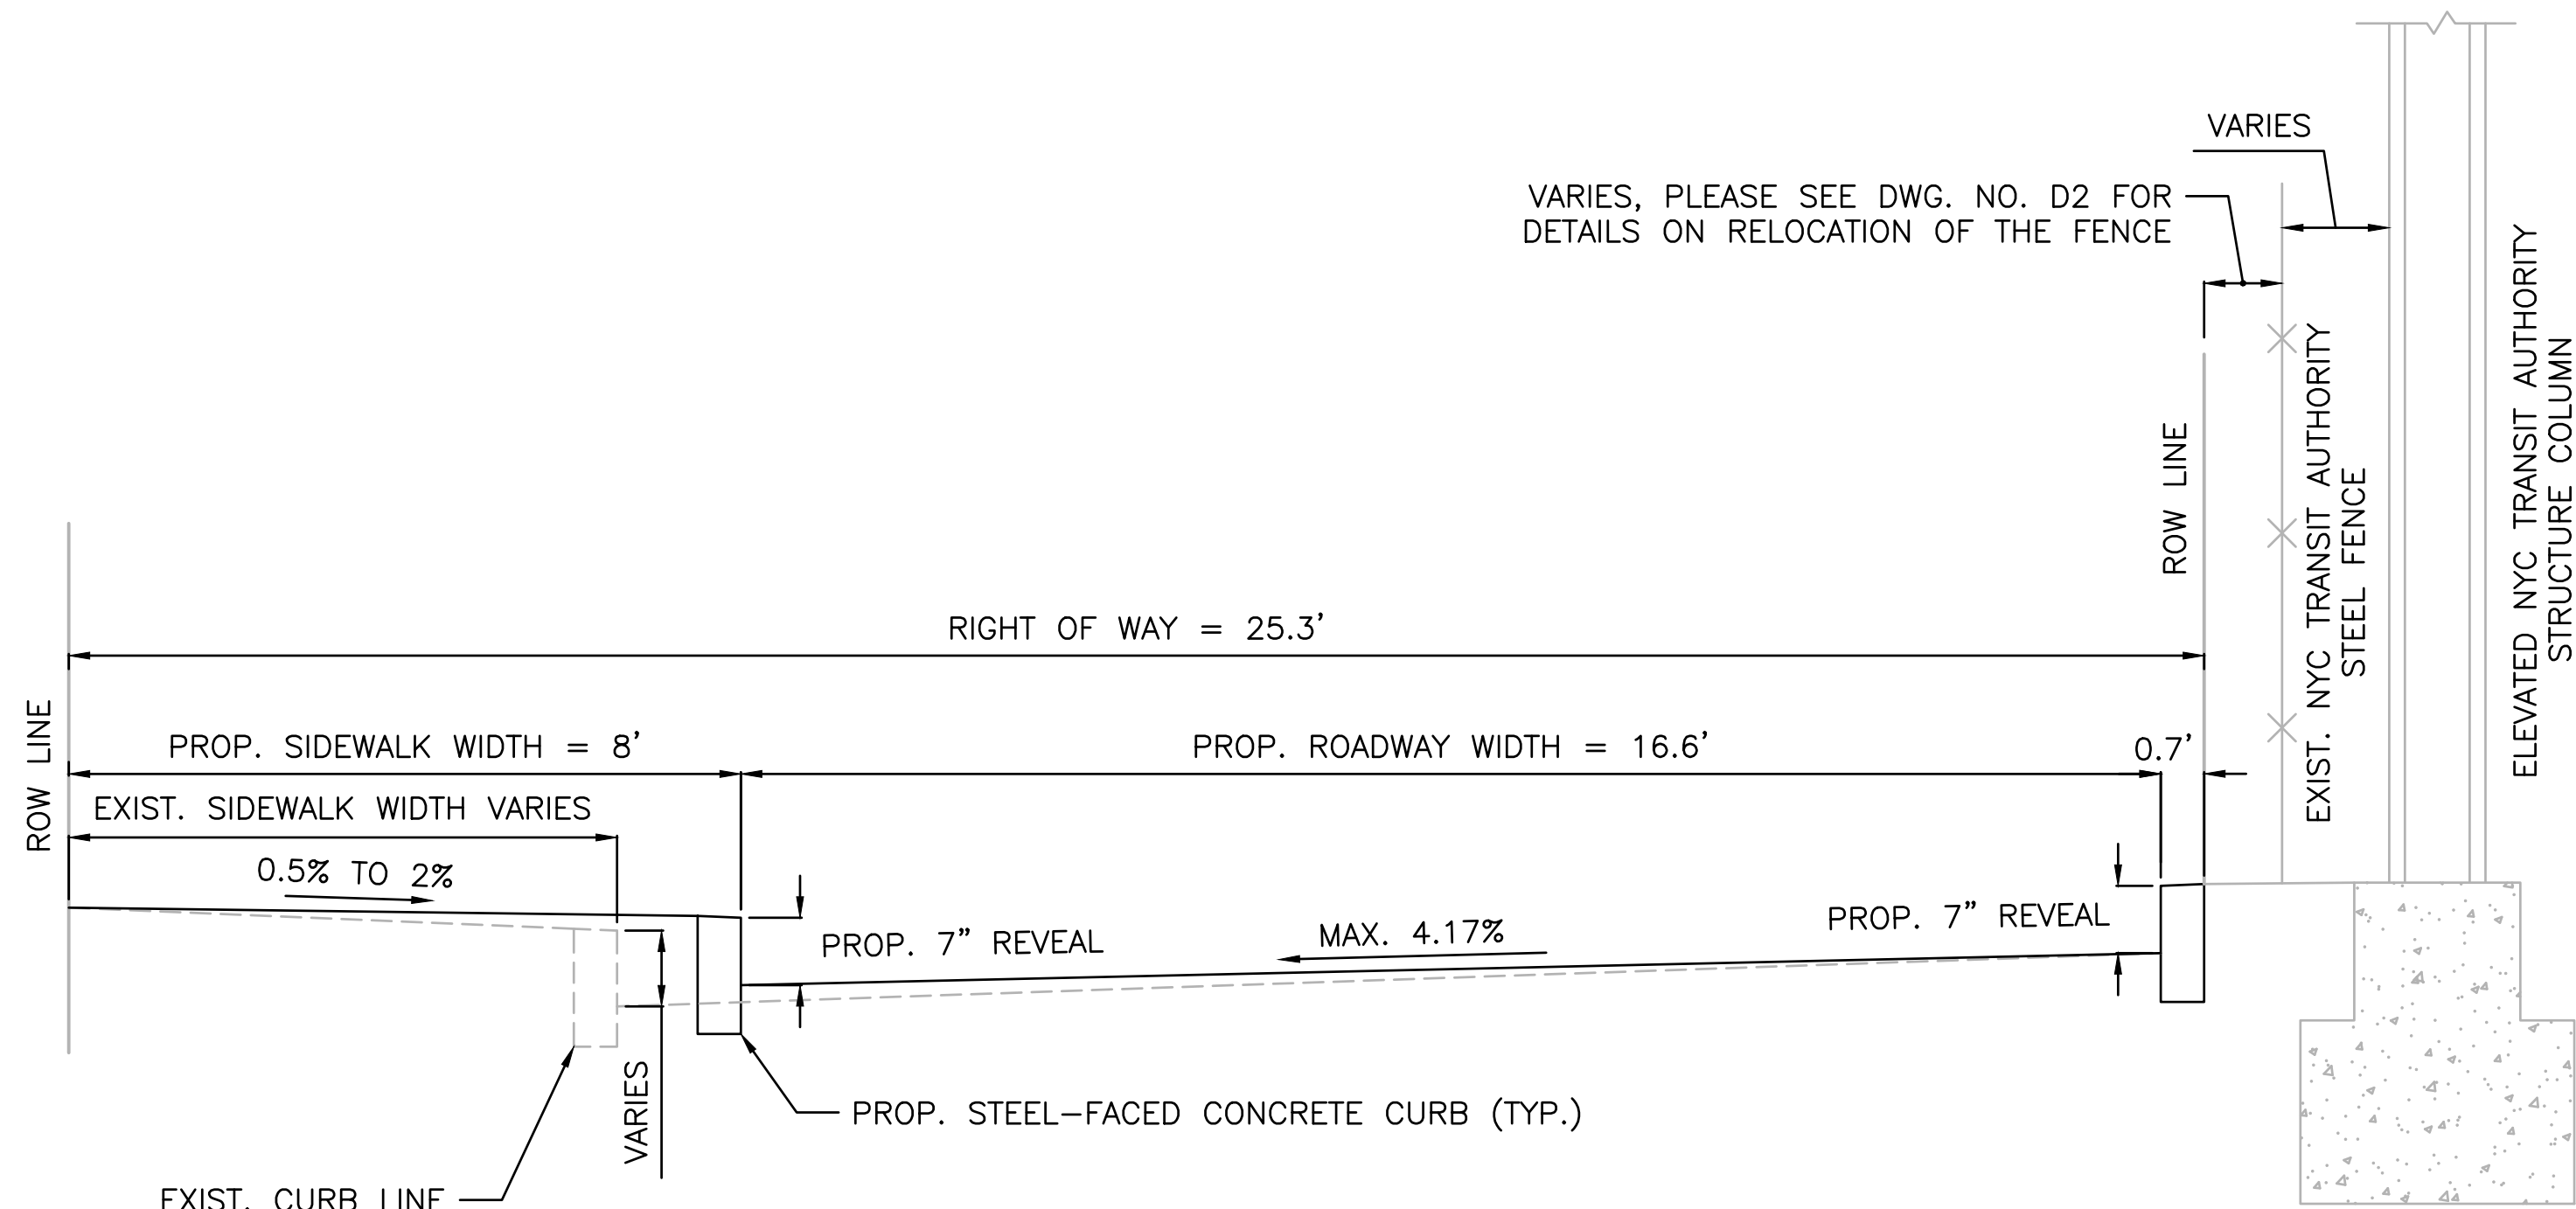

DETAIL #1
TYPICAL ROADWAY CROSS-SECTION
ALONG VAN SINDEREN AVENUE LOOKING SOUTH
SCALE: N.T.S.

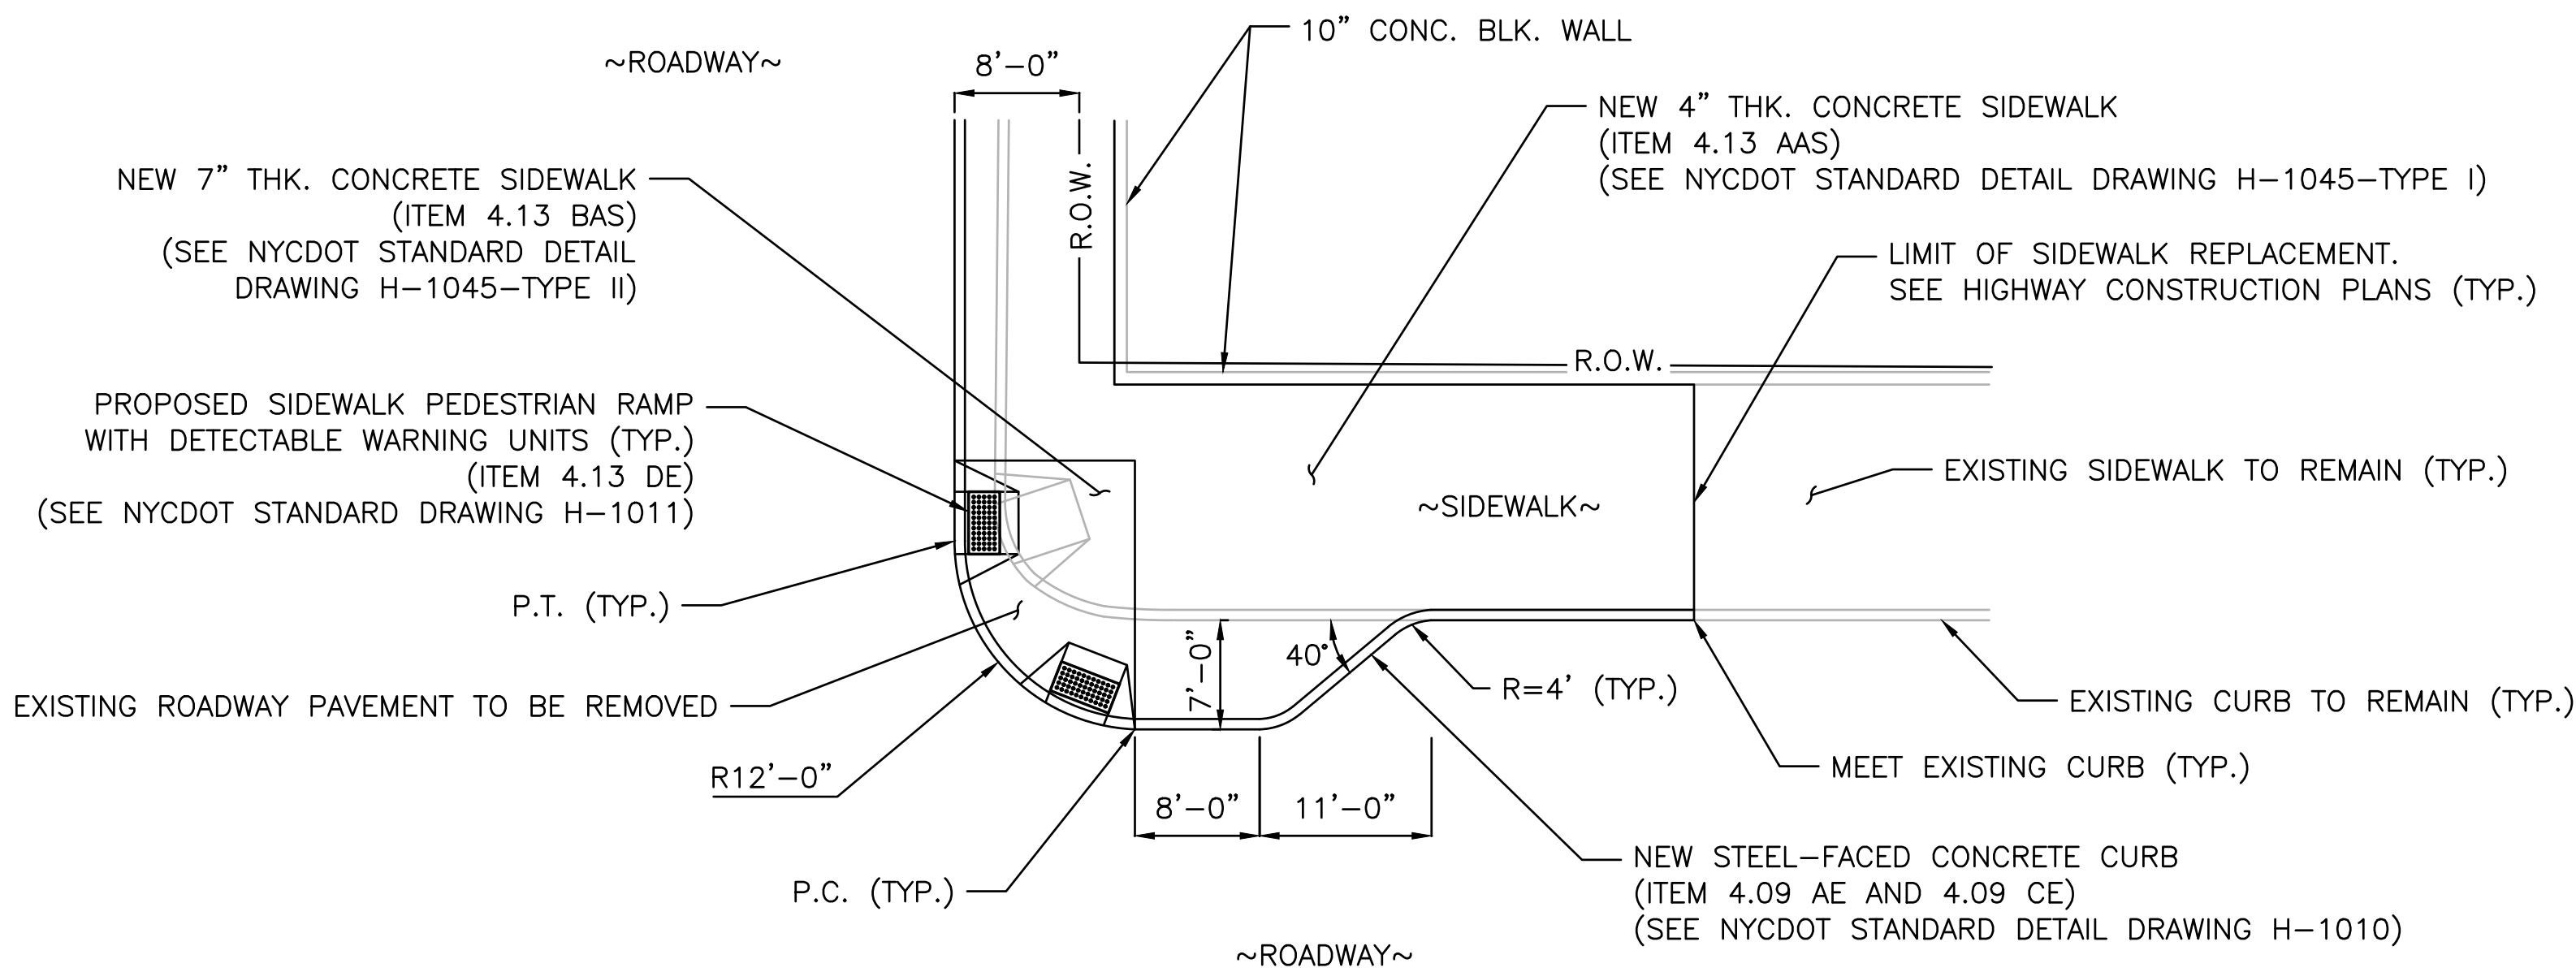


DETAIL #3
TYPE 1 NECK DOWN DETAIL FOR
VAN SINDEREN AVENUE AND SUTTER AVENUE (NE CORNER)
SCALE: N.T.S.

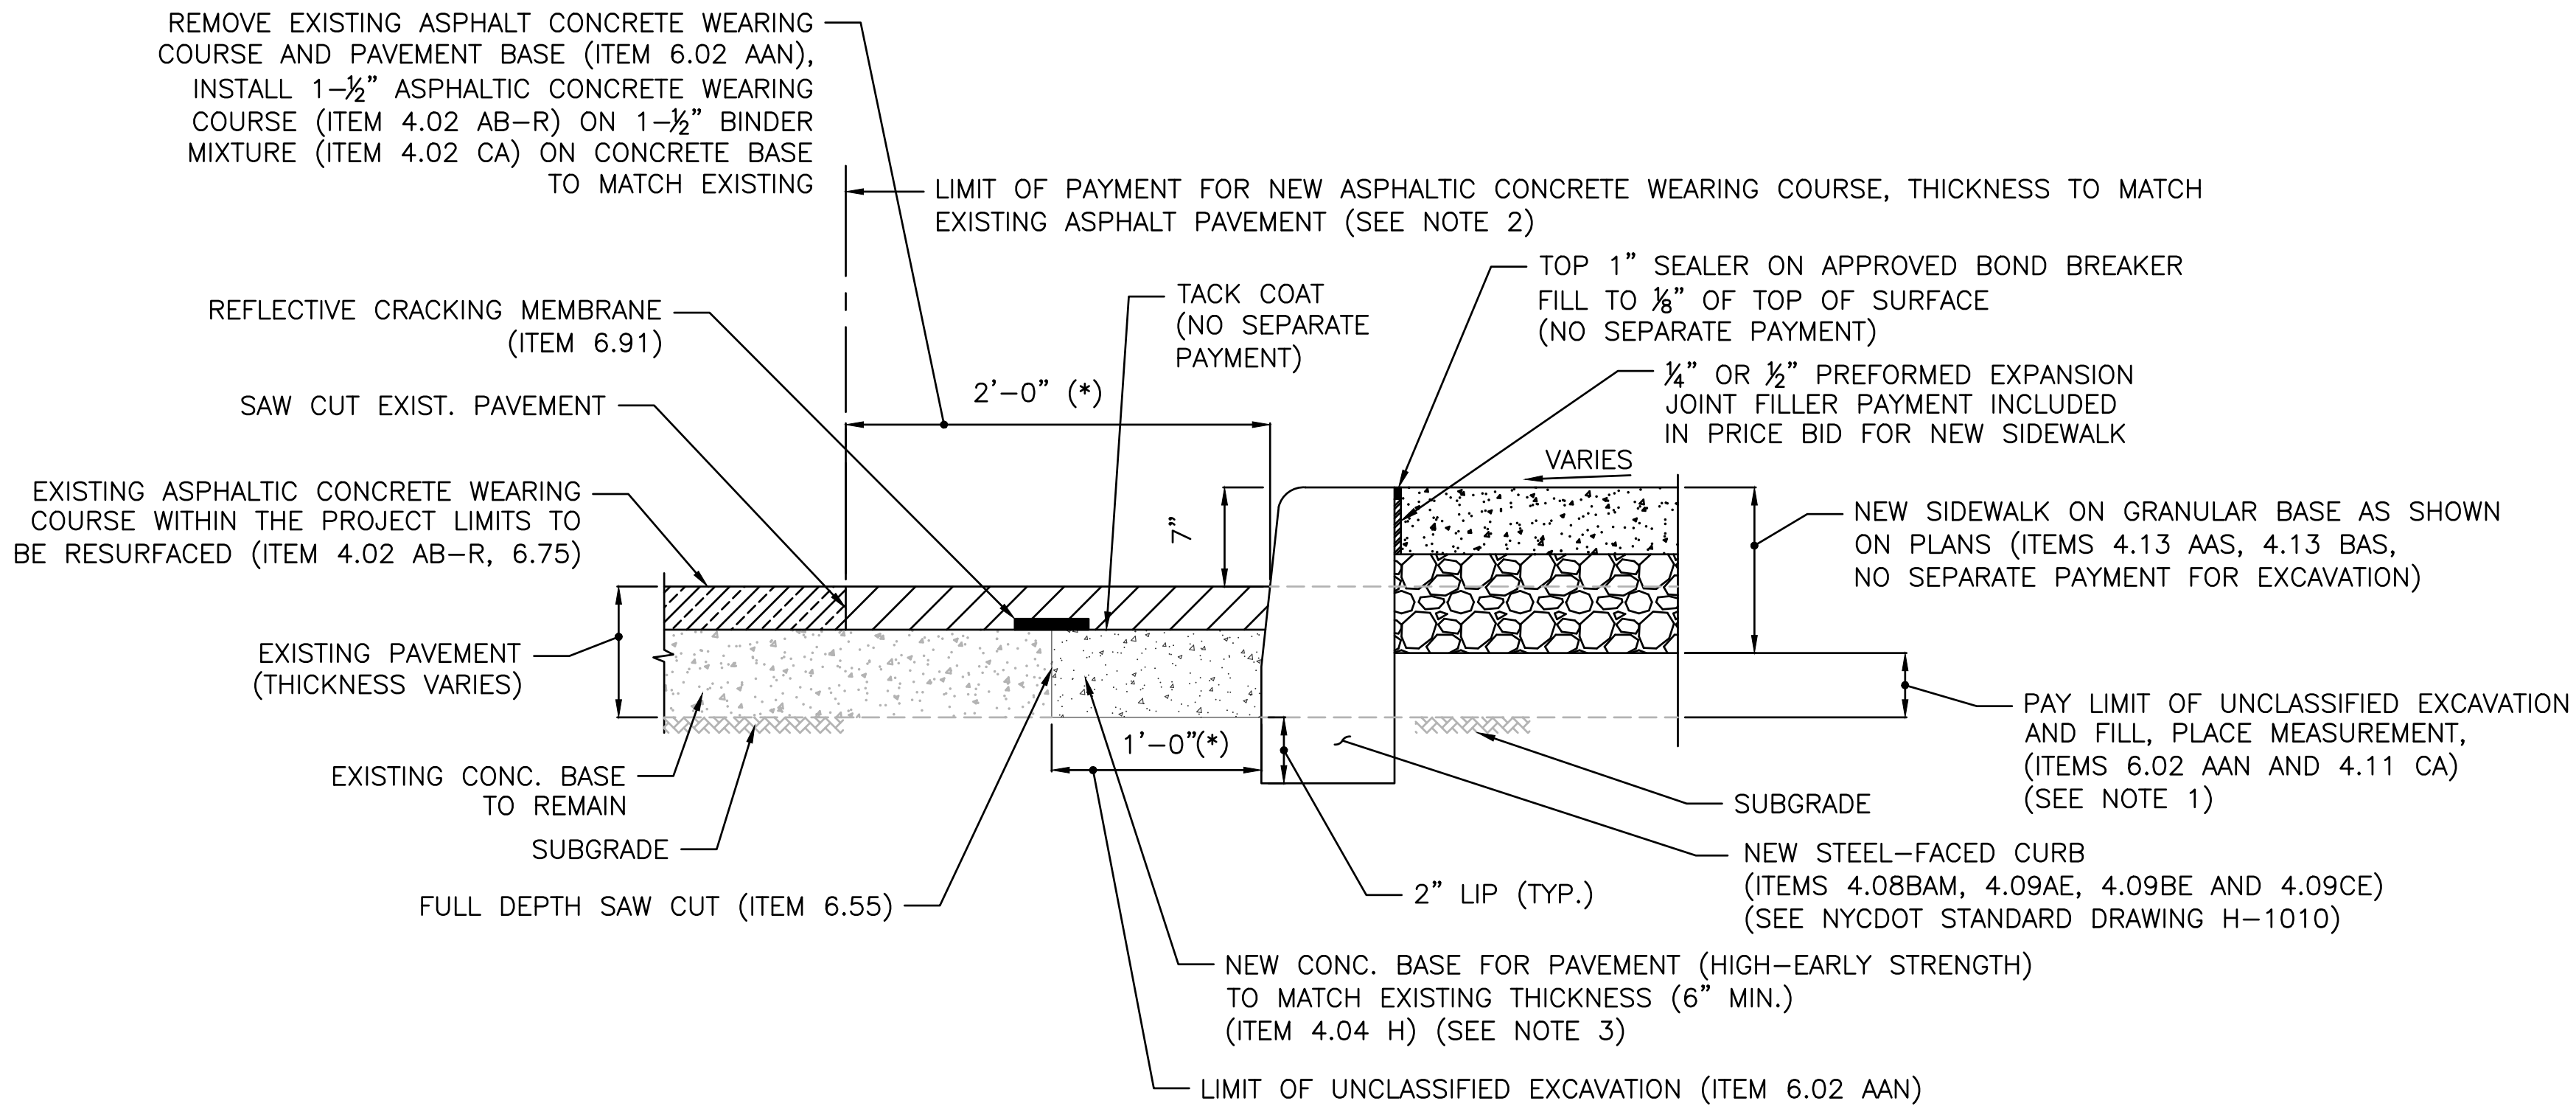

DETAIL #2
CURB, SIDEWALK, AND PAVEMENT DETAIL
SCALE: N.T.S.

- NOTES:
- EXCAVATE EXISTING ROADWAY PAVEMENT AND PLACE FILL TO THE BOTTOM OF SIDEWALK GRANULAR BASE AS REQUIRED FOR INSTALLATION OF NEW SIDEWALK.
 - IF THICKNESS OF EXISTING PAVEMENT WEARING COURSE IS LESS THAN 3", CONTRACTOR SHALL PROVIDE 1-1/2" ASPHALTIC CONCRETE WEARING COURSE (ITEM 4.02 AB-R) WITH BINDER MIXTURE (ITEM 4.02 CA) TO MATCH EXISTING THICKNESS.
 - SUBBASE AND PLASTIC FILTER FABRIC TO BE PLACED ONLY IF DIRECTED BY ENGINEER. TO BE PAID FOR UNDER SUBBASE COURSE, SELECT GRANULAR MATERIAL, ITEM NO. 6.67 AND PLASTIC FILTER FABRIC, ITEM NO. 6.68.
- (*) OR AS ORDERED BY THE ENGINEER.

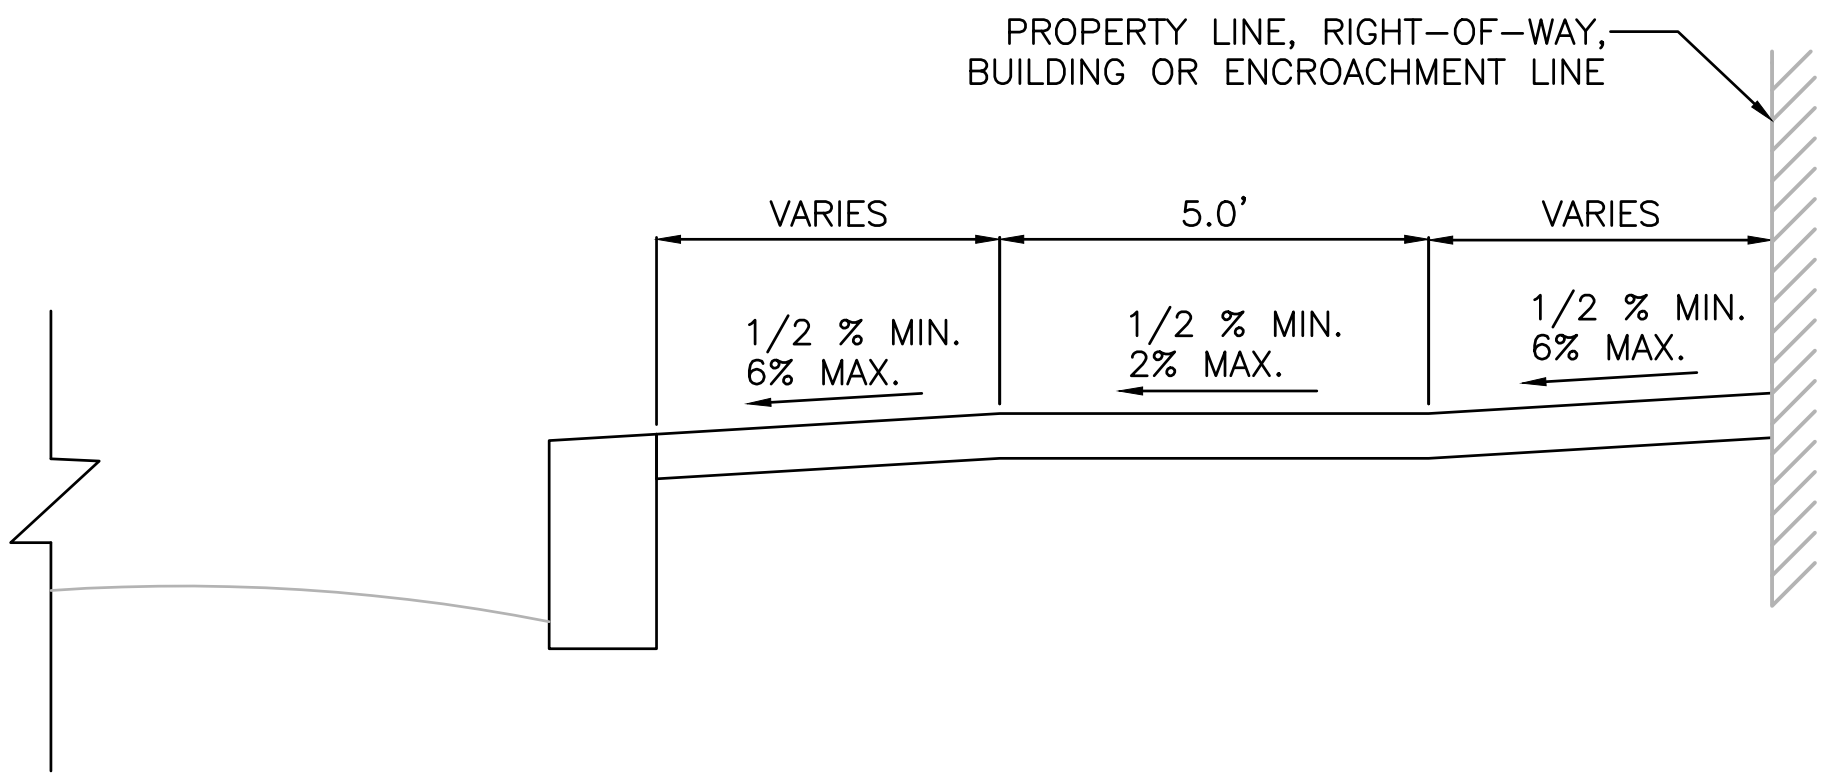

DETAIL #4
TYPICAL FULL WIDTH SIDEWALK SECTION
ADA COMPLIANCE
SCALE: N.T.S.

NOTE:
NEW SIDEWALKS SHALL BE CONSTRUCTED TO MEET EXISTING CONDITIONS AT THE PROPERTY LINE, ROW-OF-WAY, BUILDING, OR ENCROACHMENT LINE (DRIVEWAYS, WALKWAYS, ETC.). THE CONTRACTOR SHALL SITE-ADAPT SIDEWALK CROSS-SLOPE TO MEET ADA CRITERIA.

FINAL DESIGN PREPARED BY:
GANDHI ENGINEERING, INC.
CONSULTING ENGINEERS
111 JOHN STREET
NEW YORK, N.Y. 10038

SIGNATURE

DATE

TOPOGRAPHIC SURVEY PREPARED BY:
LICENSED LAND SURVEYOR


DRAWN BY: KK
CADD FILE:
Typical Details.dwg
August 11, 2026-7:34PM

SCALE
NOT TO SCALE

CITY OF NEW YORK
DEPARTMENT OF DESIGN + CONSTRUCTION
DIVISION OF INFRASTRUCTURE
BUREAU OF DESIGN


TYPICAL DETAILS - 1

NO.	DATE	DESCRIPTIONS REVISIONS	BY	APPR'D
VAN SINDEREN AVENUE STREETSCAPE IMPROVEMENTS BOROUGH OF BROOKLYN				
PROJECT ID: NDF-IBZ		DATE: 04/01/2019	SHEET 3 OF 22	D1 07

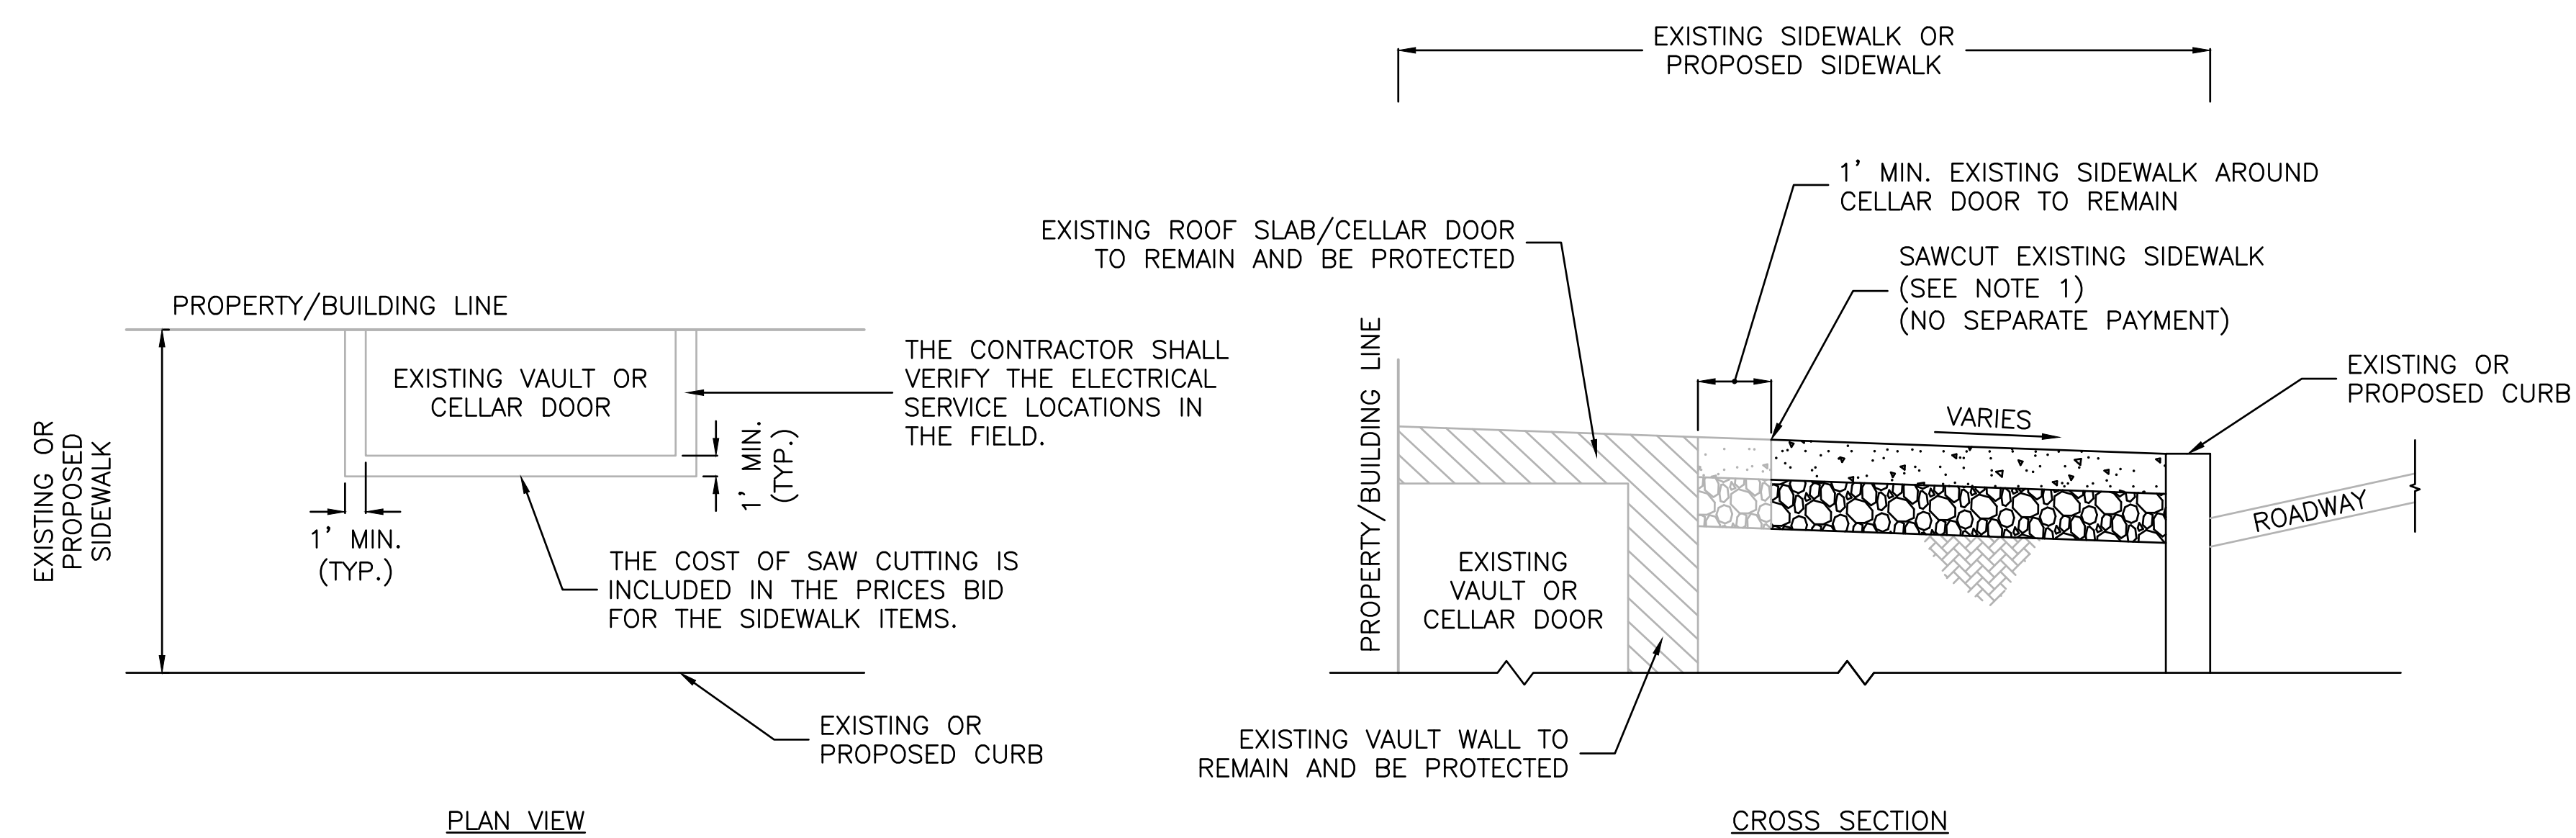


- NOTES:

1. THE CONTRACTOR SHALL VERIFY THE LOCATION AND EXTENT OF THE VAULTS WITHIN THE PROJECT LIMITS BEFORE THE START OF CONSTRUCTION.
2. THE CONTRACTOR SHALL DETERMINE THE ACTUAL LOCATION FOR THE SAW CUT LINE SO THAT IT DOES NOT IMPACT THE EXISTING VAULT OR CELLAR DOOR. THE CONTRACTOR SHALL EXERCISE CAUTION IN THIS AREA TO INSURE THAT THE VAULT OR CELLAR DOOR IS NOT DISTURBED. ANY DAMAGES SHALL BE REPAIRED AT THE CONTRACTOR'S EXPENSE TO SATISFACTION OF THE ENGINEER.

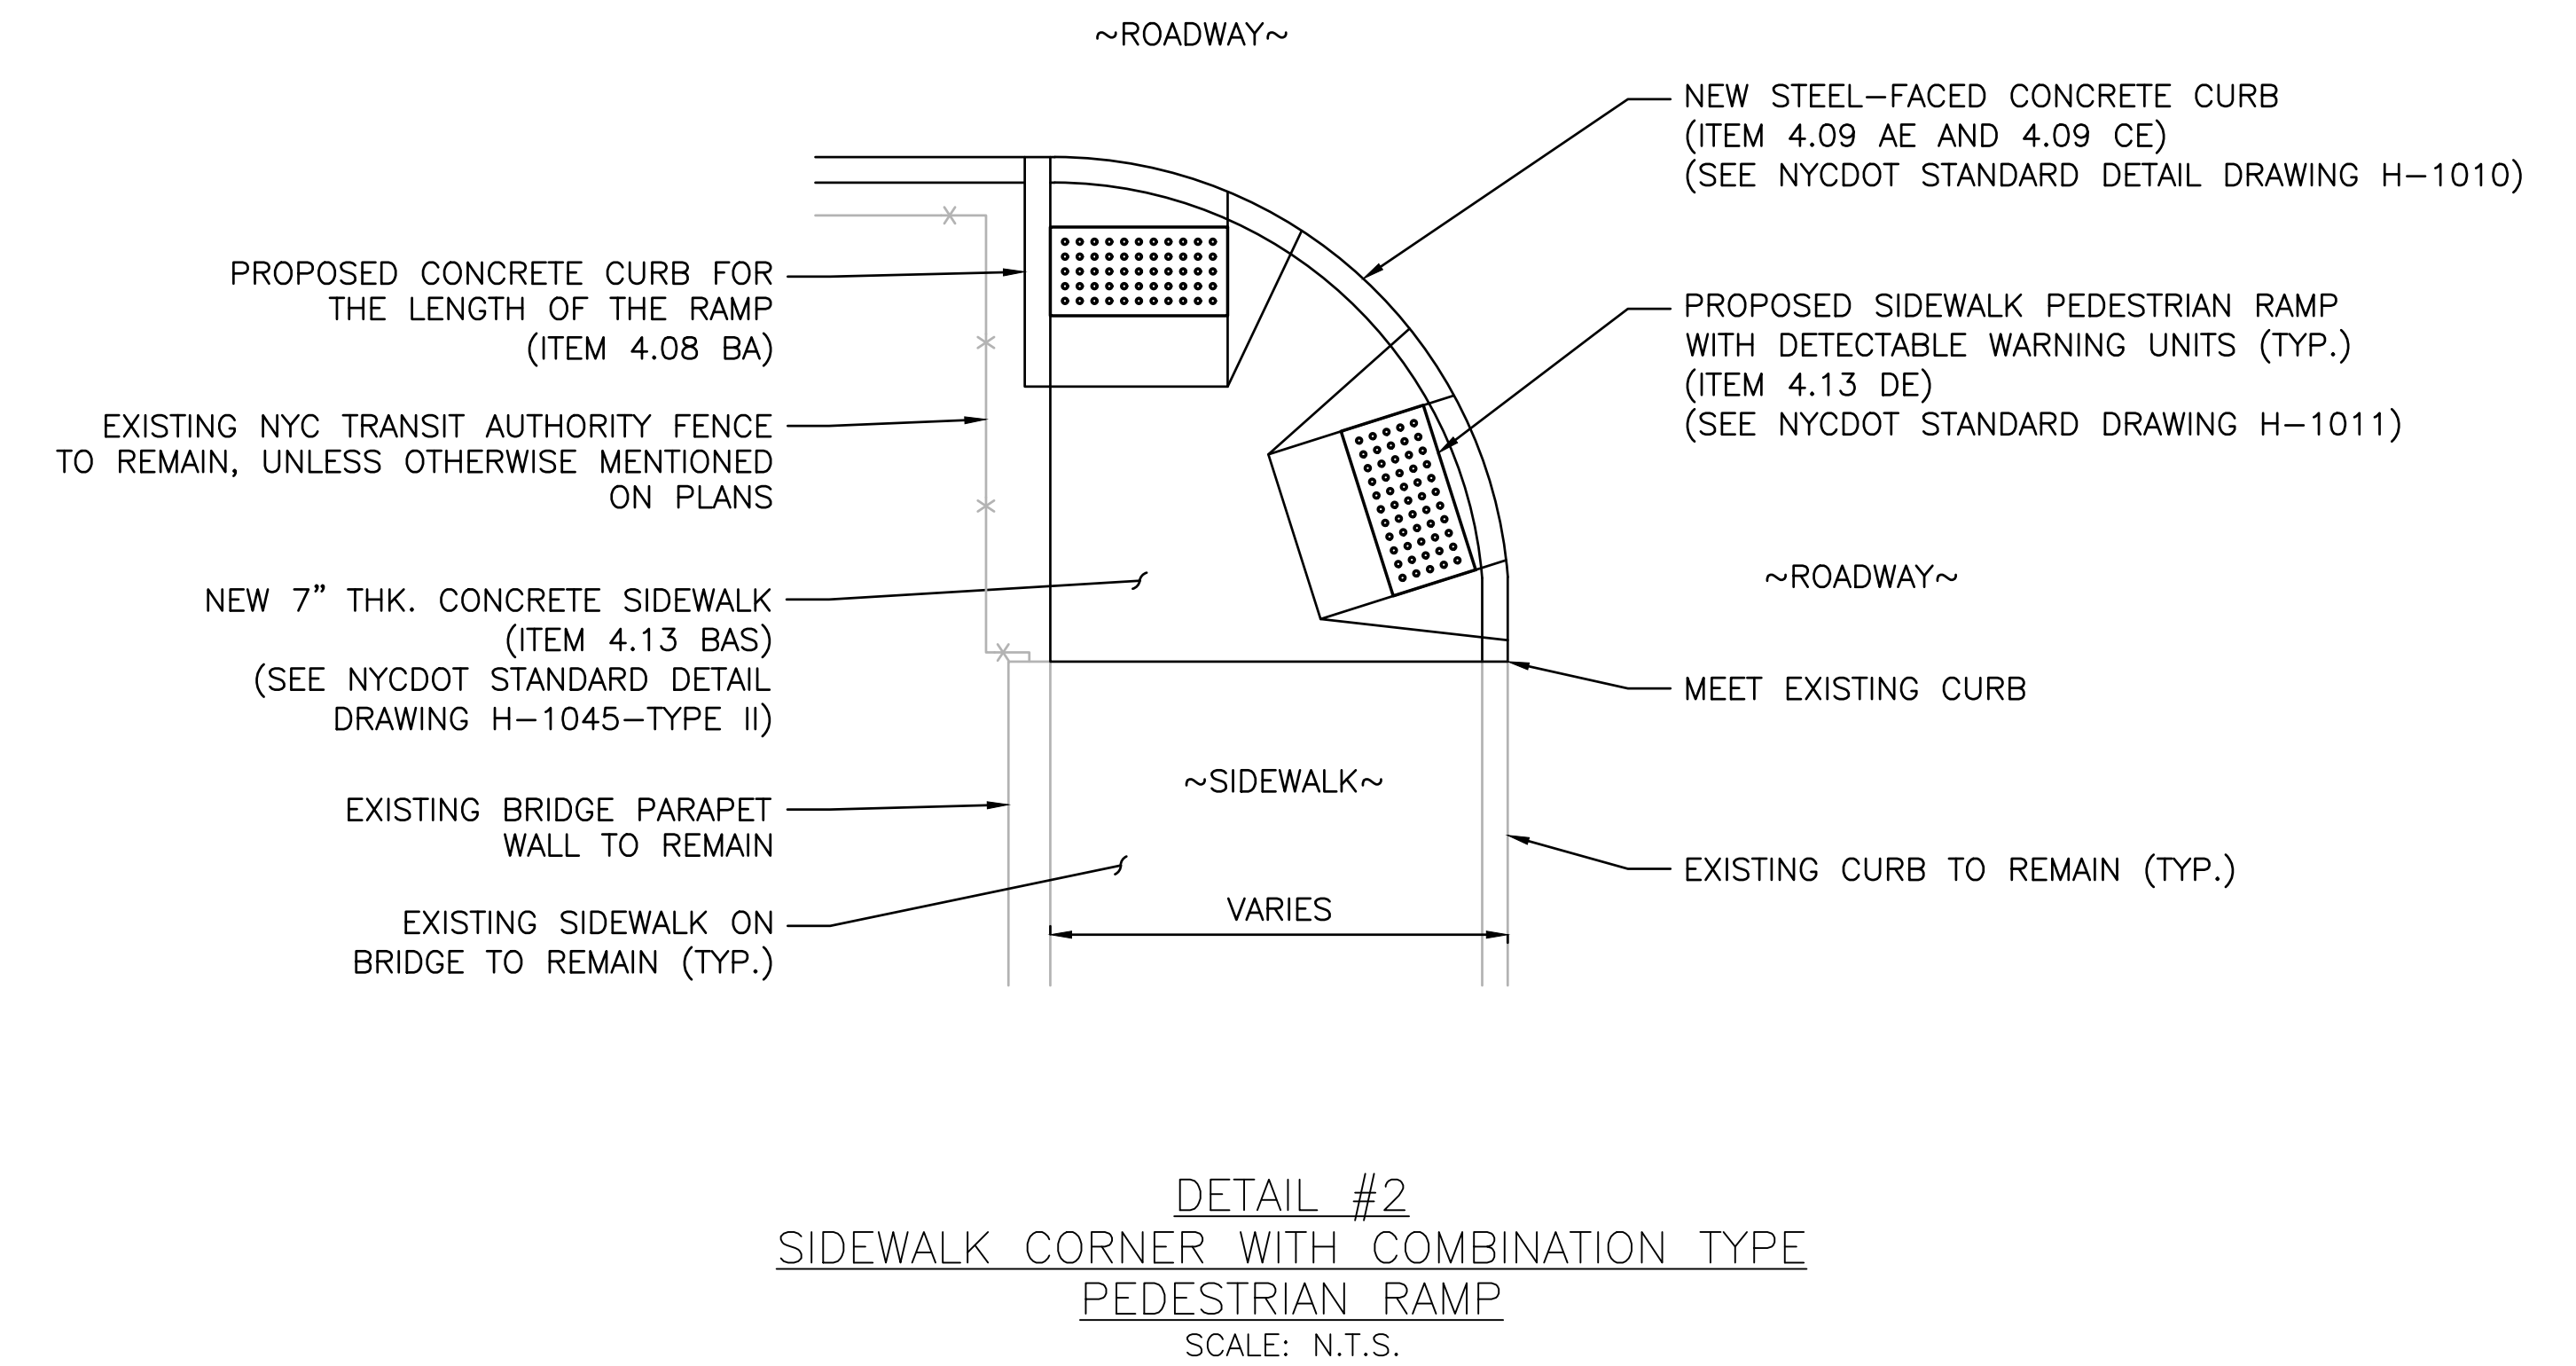

- NOTES:


1. PROPOSED LOCATIONS WITH COMBINATION TYPE PEDESTRIAN RAMP:
NW AND SW CORNER OF VAN SINDEREN AVENUE AND LIBERTY AVENUE INTERSECTION
NW AND SW CORNER OF VAN SINDEREN AVENUE AND GLENMORE AVENUE INTERSECTION

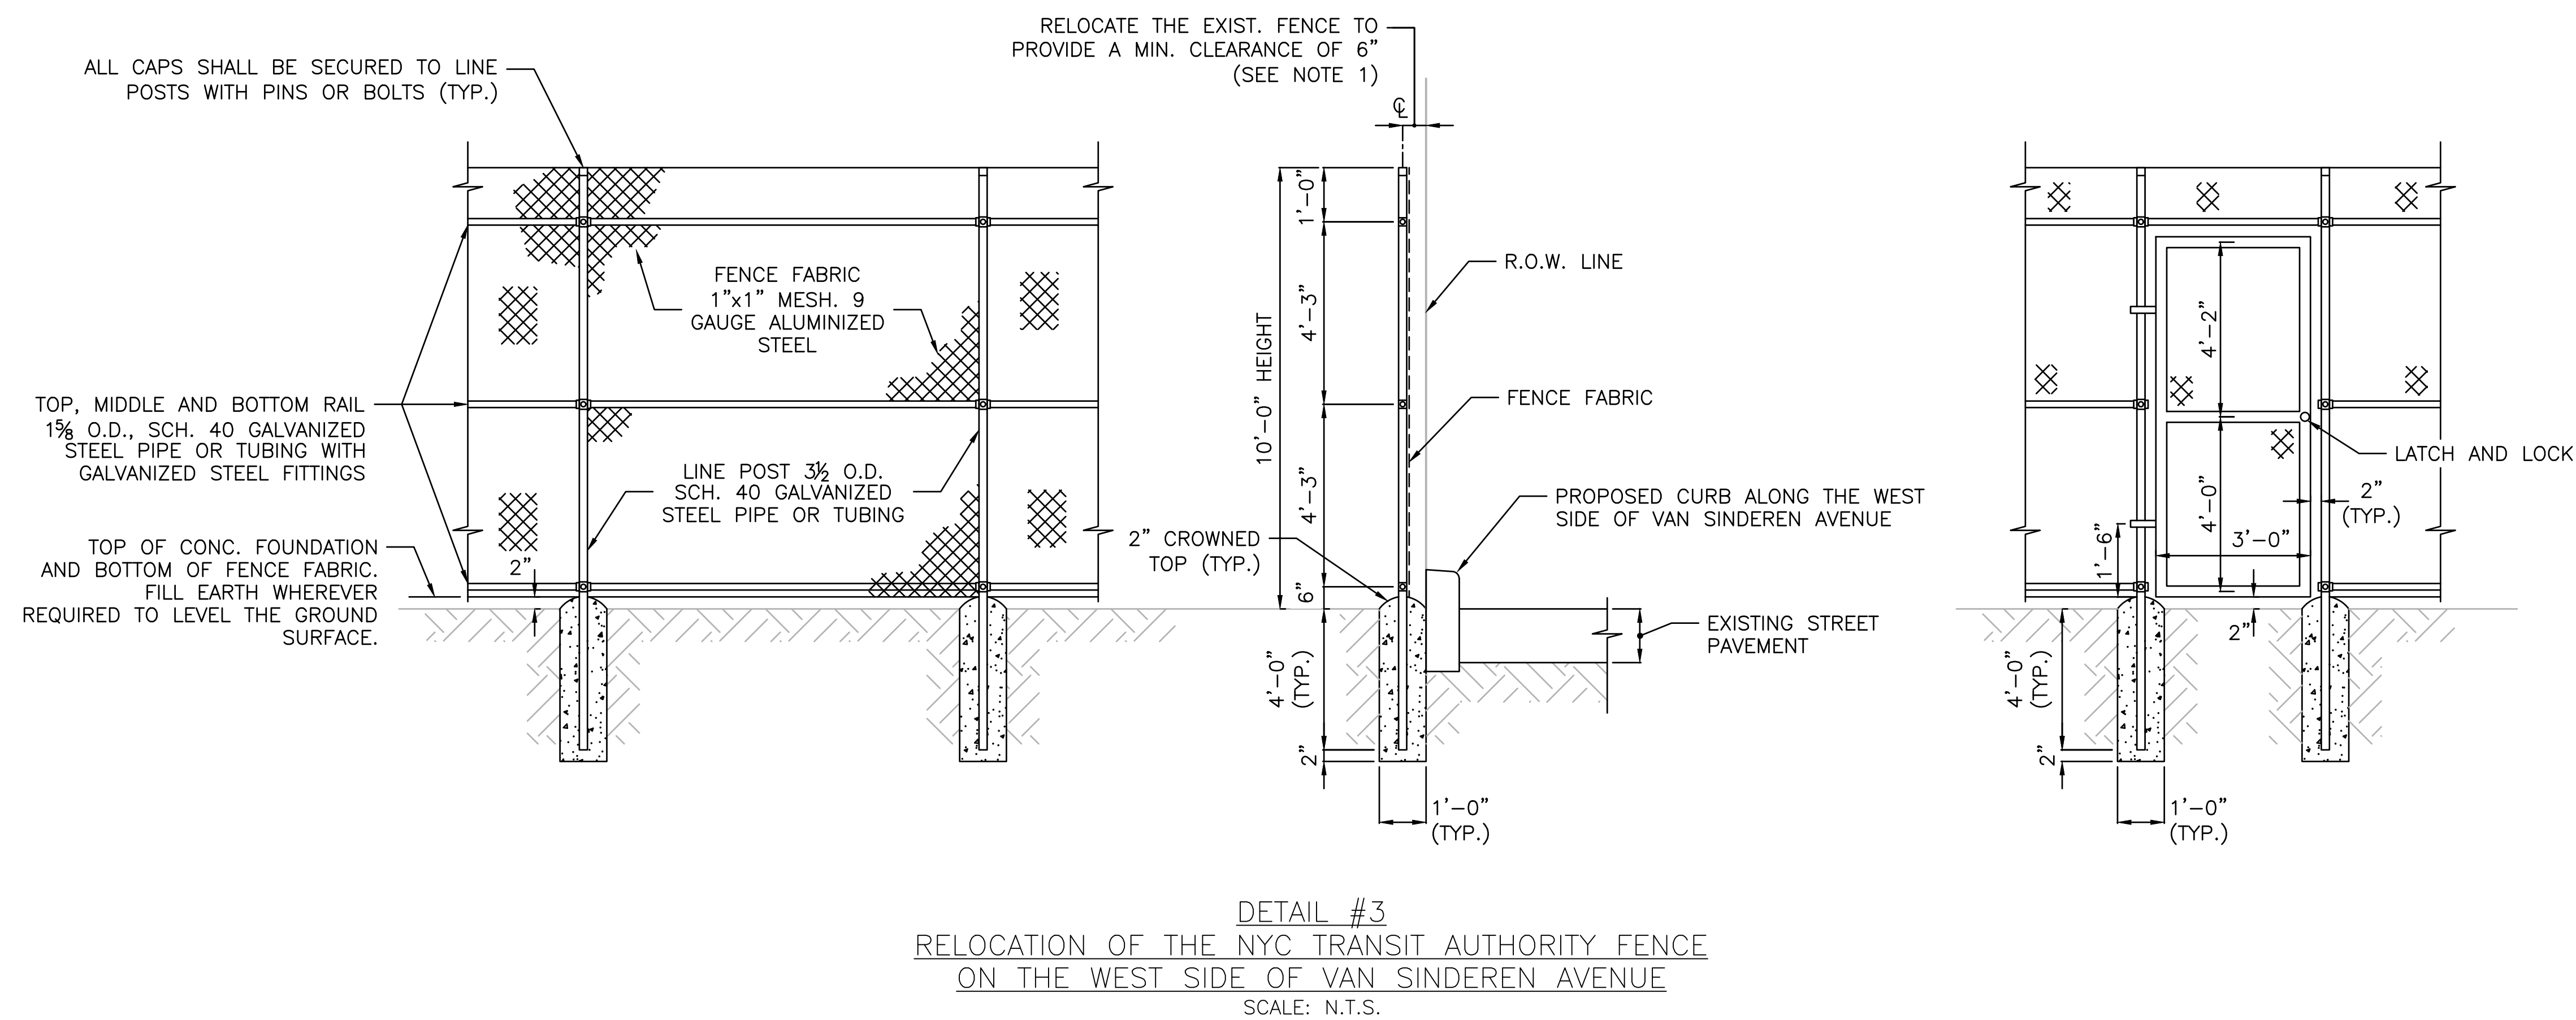


- NOTES:

1. FOR THE LIMITS OF NYC TRANSIT AUTHORITY FENCE RELOCATION, PLEASE REFER TO THE CONSTRUCTION PLANS.
2. THE CONTRACTOR IS NOTIFIED THAT THERE SHALL BE NO MACHINE EXCAVATION WITHIN 3'-0" (THREE FEET) OF NYC TRANSIT STRUCTURES, POWER DUCT LINES, OR ANY OTHER FACILITIES UNTIL THEY HAVE BEEN CAREFULLY EXPOSED BY HAND EXCAVATION.
3. ANY DAMAGE TO SUBWAY STRUCTURE AND FENCE DURING RELOCATION WILL BE REPAIRED BY THE CONTRACTOR AT NO COST TO THE CITY AND TO THE SATISFACTION OF THE NYC TRANSIT AUTHORITY INSPECTOR.


NO.	DATE	DESCRIPTIONS REVISIONS	BY	APPR'D	
VAN SINDEREN AVENUE STREETSCAPE IMPROVEMENTS BOROUGH OF BROOKLYN					
PROJECT ID: NDF-IBZ		DATE: 04/01/2019	SHEET 4	OF 22	D2/D7

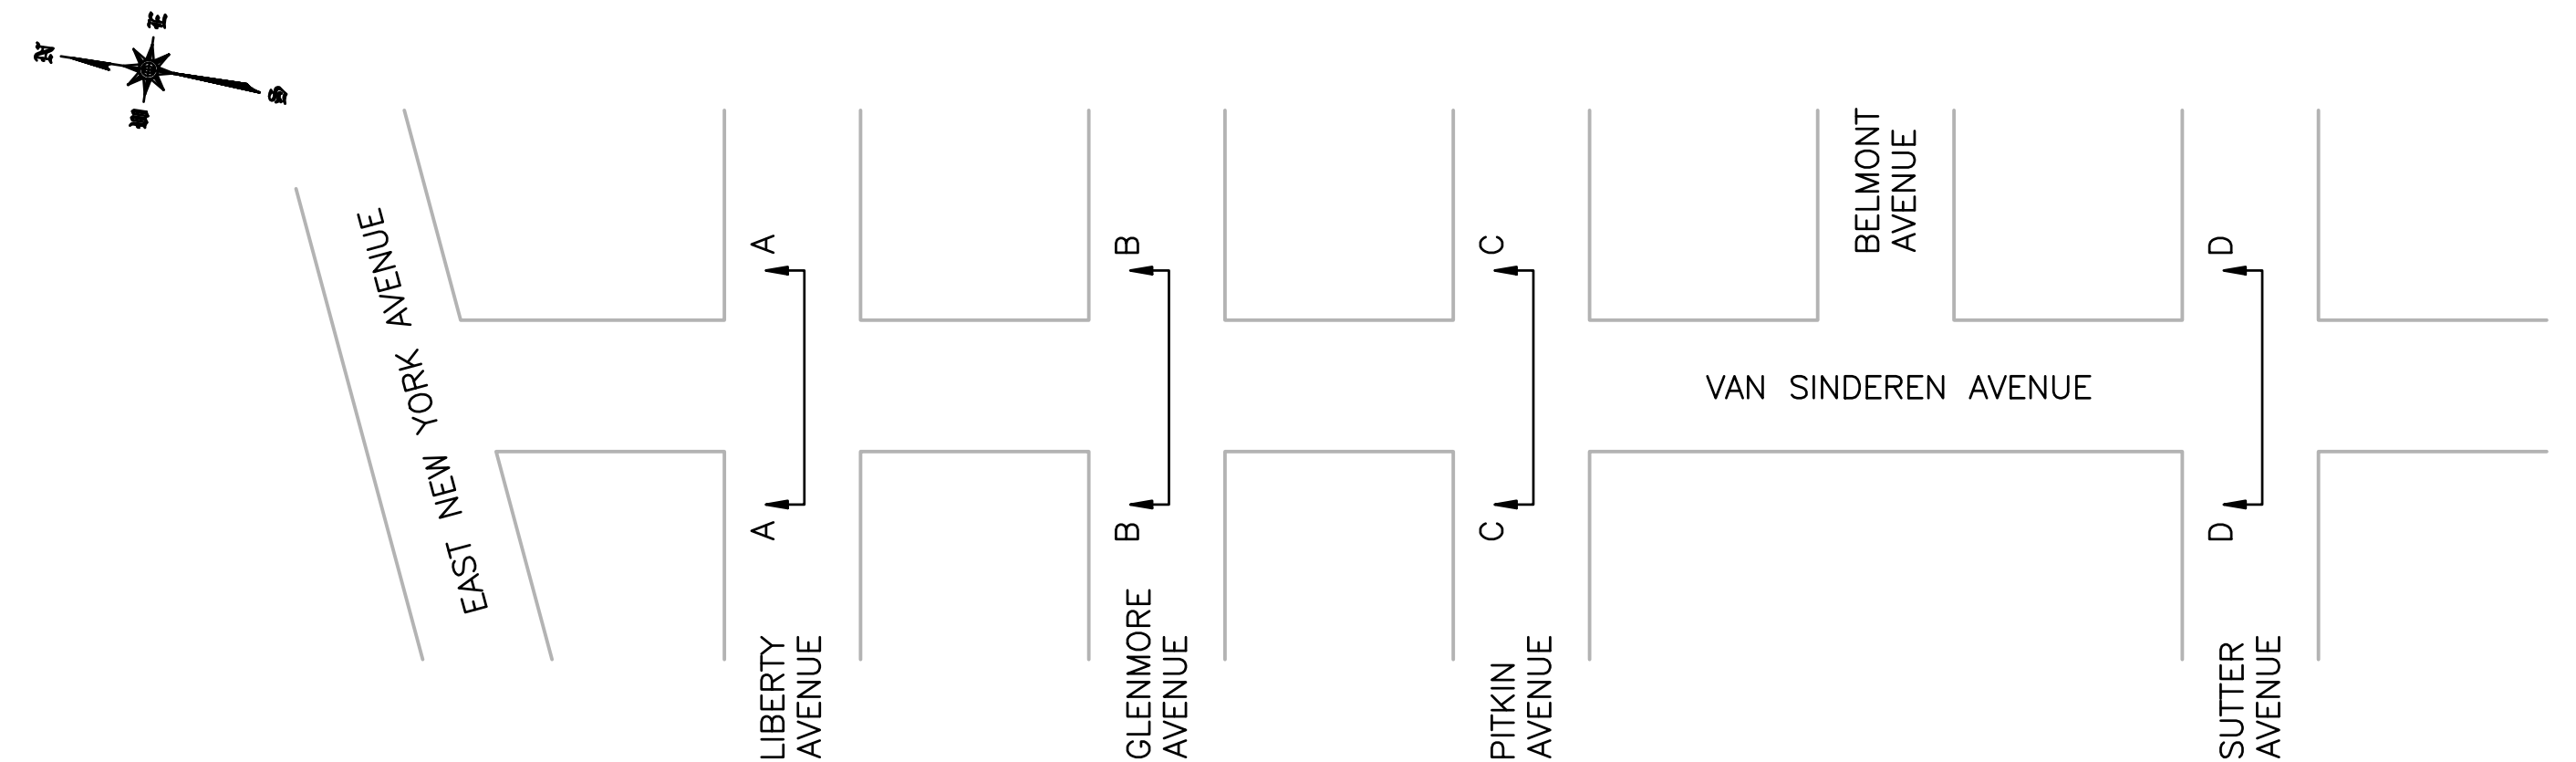


DETAIL #1
SECTION LOCATION PLAN
SCALE: N.T.S.

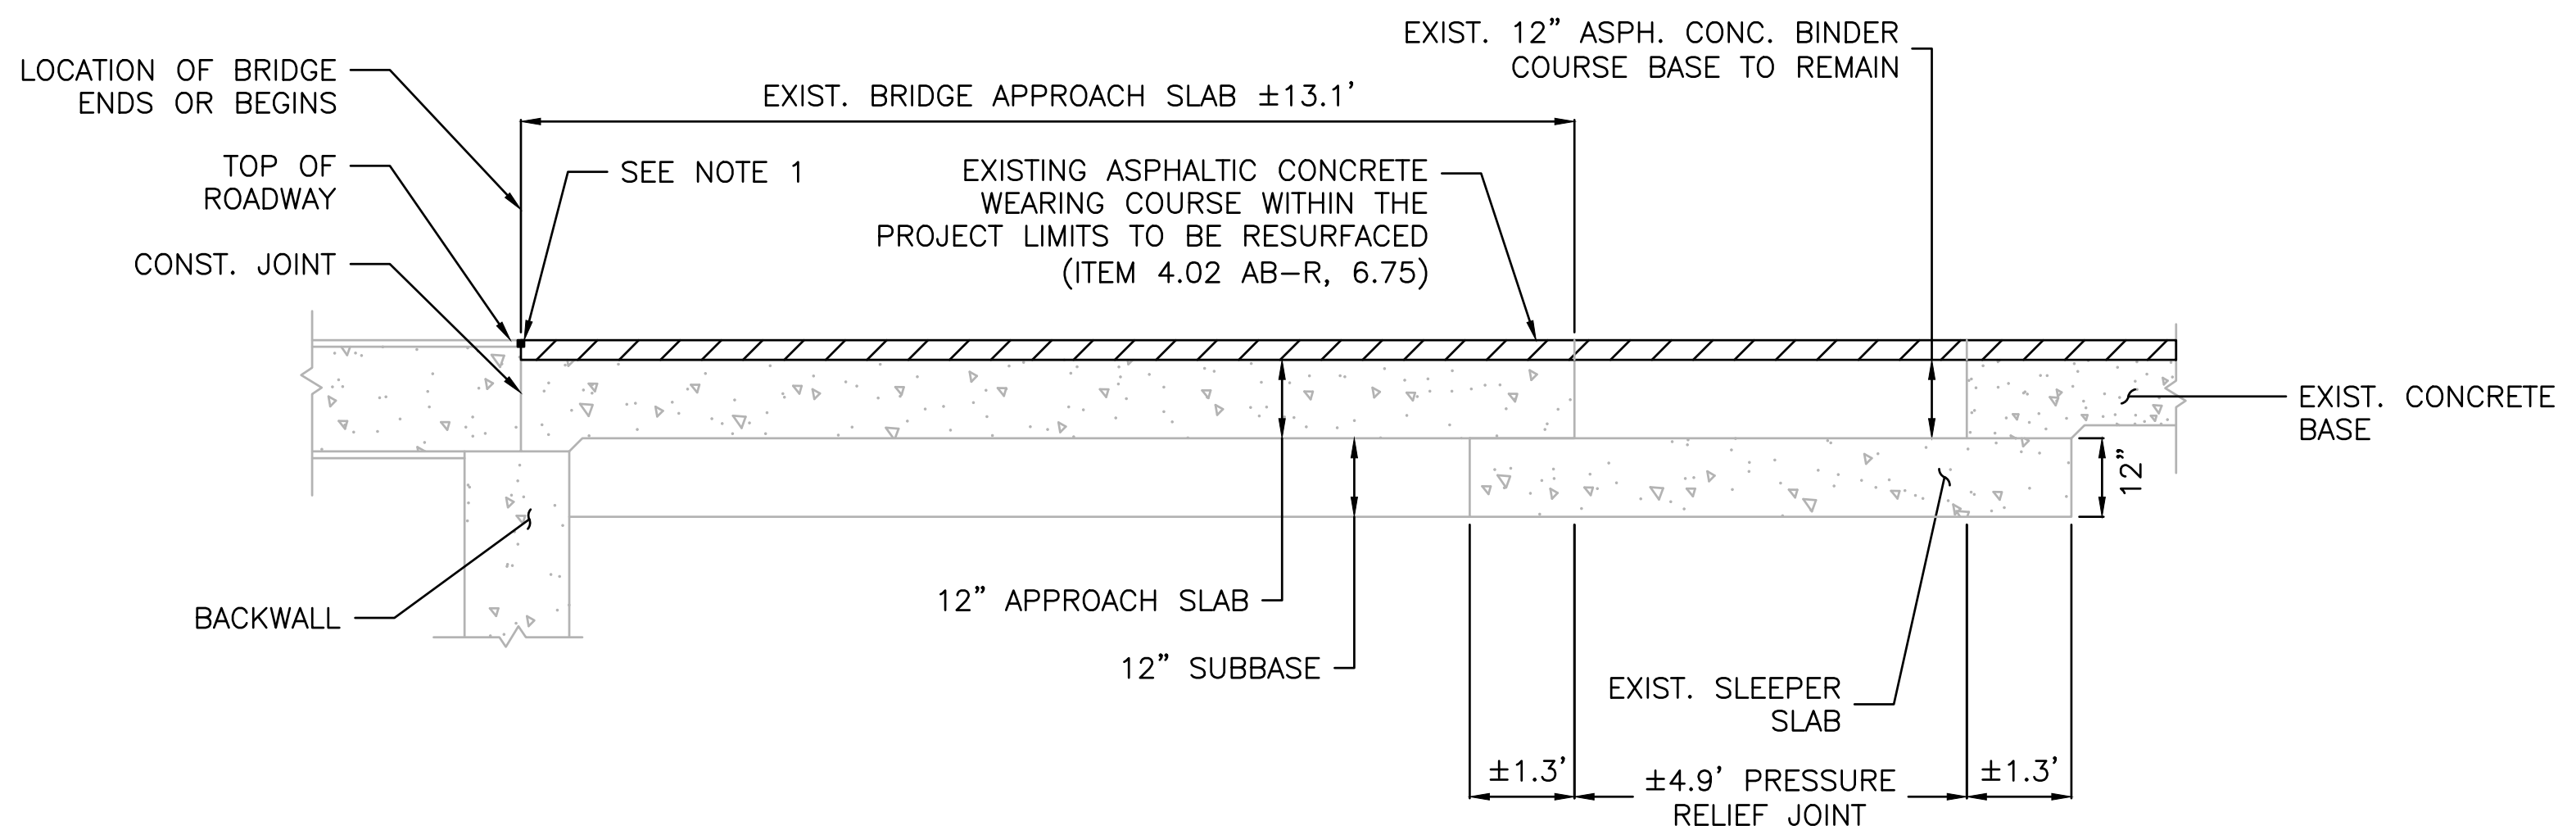


DETAIL #2
SECTION A-A: APPROACH SLAB AT
LIBERTY AVENUE BRIDGE AND VAN SINDEREN
AVENUE INTERSECTION LOOKING NORTH
SCALE: N.T.S.

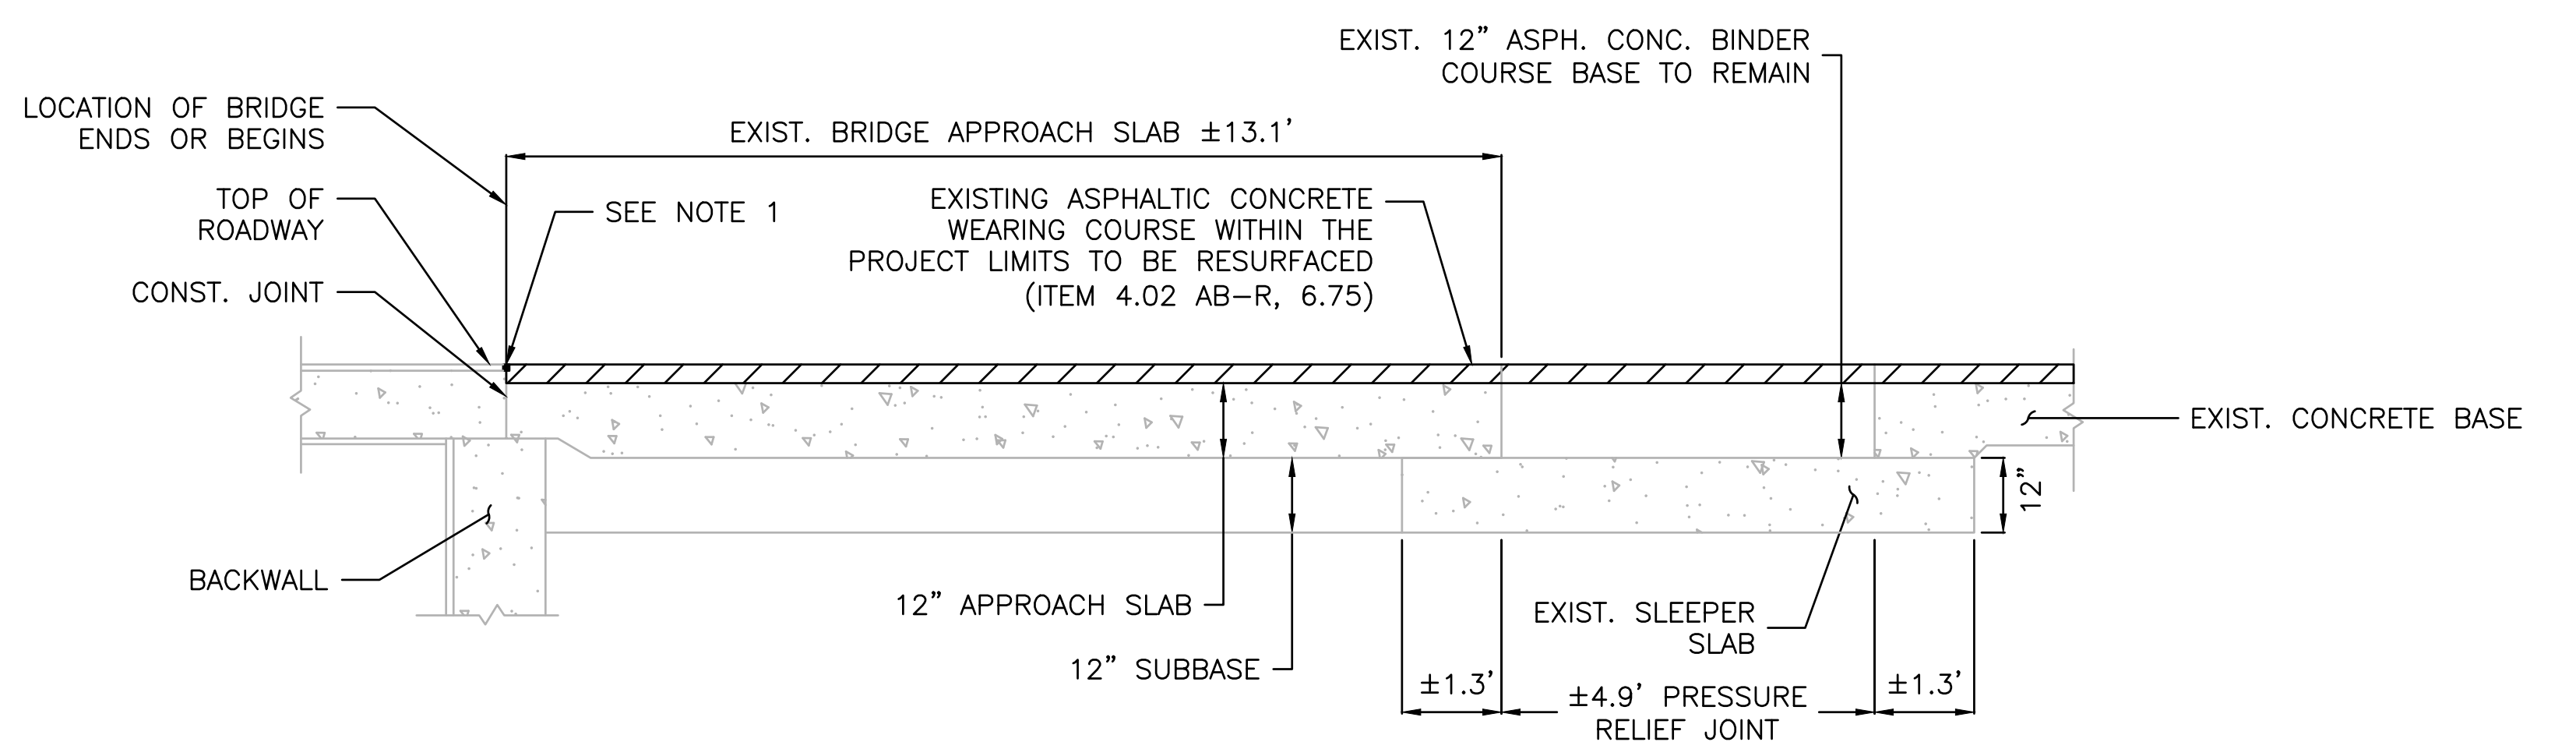

DETAIL #3
SECTION B-B: APPROACH SLAB AT
GLENMORE AVENUE BRIDGE AND VAN SINDEREN
AVENUE INTERSECTION LOOKING NORTH
SCALE: N.T.S.

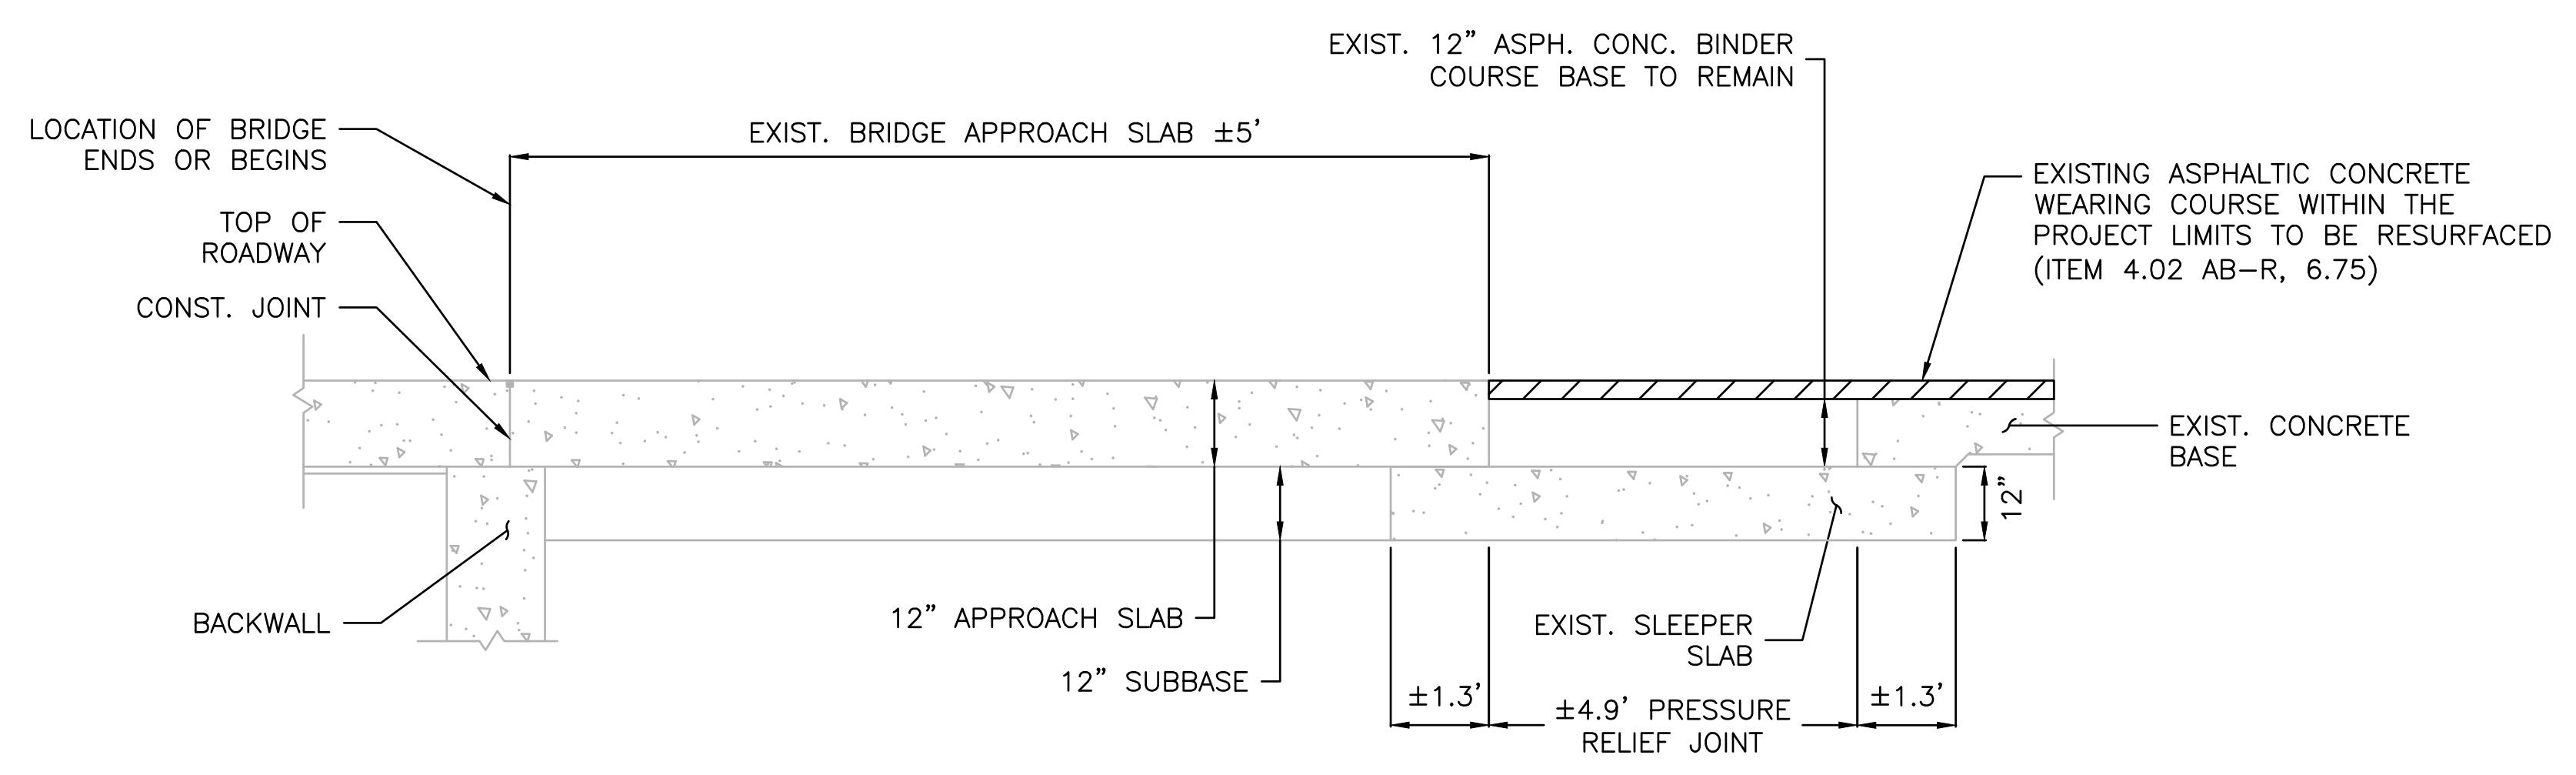

DETAIL #4
SECTION C-C: APPROACH SLAB AT
PITKIN AVENUE BRIDGE AND VAN SINDEREN
AVENUE INTERSECTION LOOKING NORTH
SCALE: N.T.S.

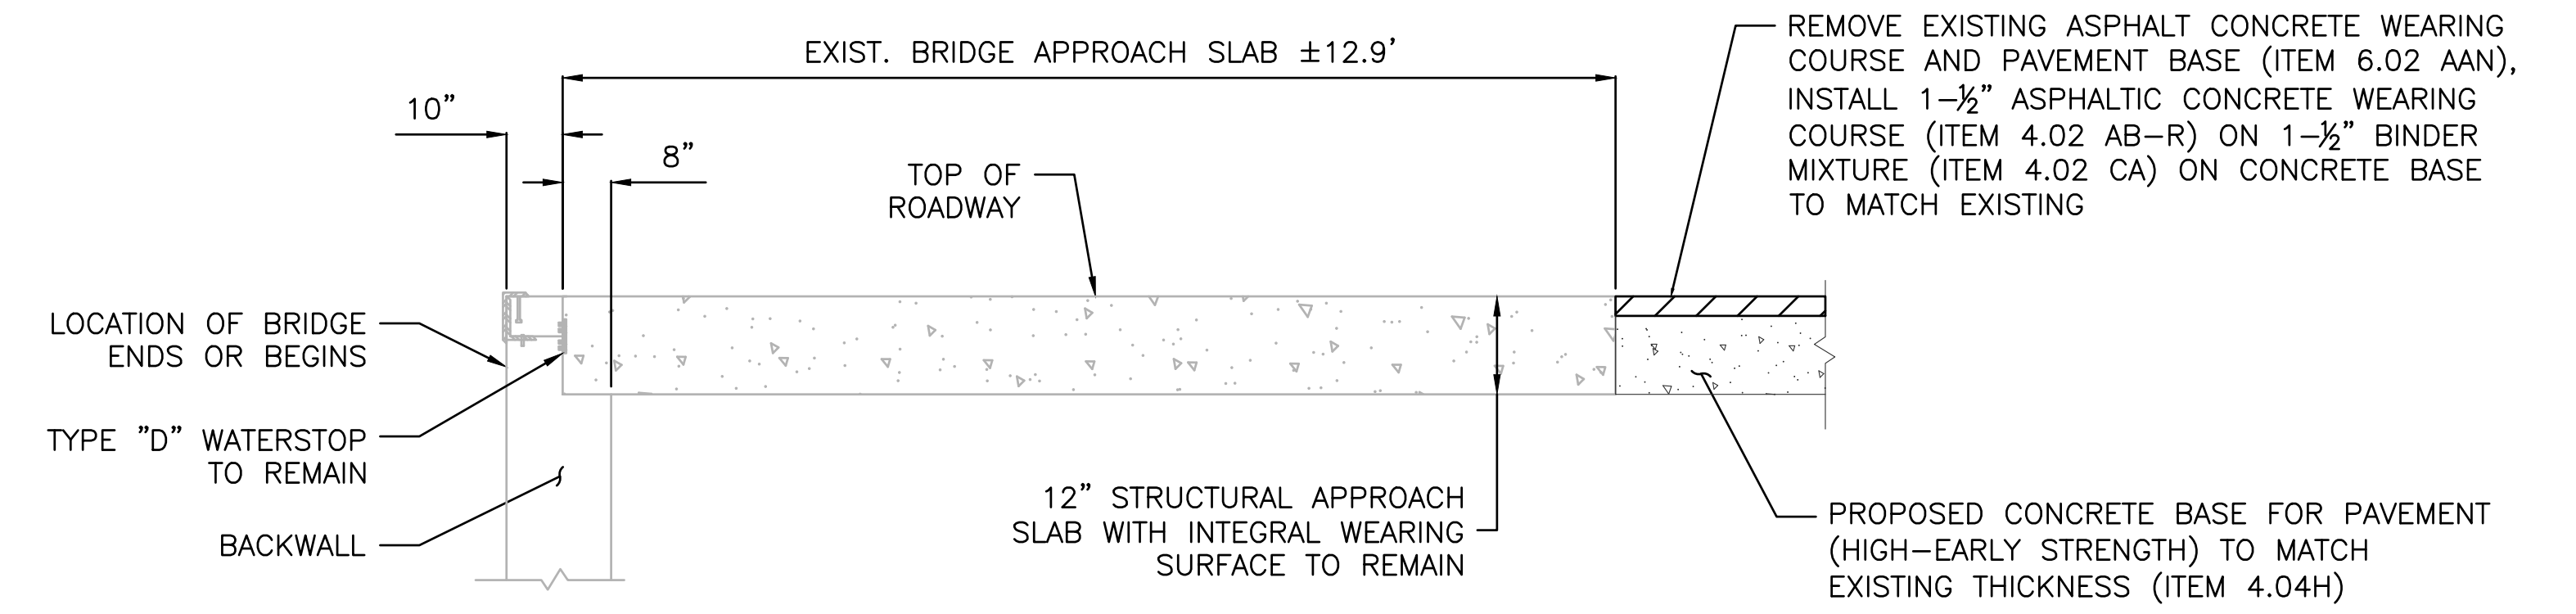

DETAIL #5
SECTION D-D: APPROACH SLAB AT
SUTTER AVENUE BRIDGE AND VAN SINDEREN
AVENUE INTERSECTION LOOKING NORTH
SCALE: N.T.S.

- NOTES:
- 0.39" X 0.78" DEEP RECESS. FILL RECESS WITH ELASTOMERIC POLYMER TYPE, TWO COMPONENT COLD APPLIED SEALER. PLACE THE SEALER IN CLEAN AIR-BLOWN NOTCH.

FINAL DESIGN PREPARED BY:
GANDHI ENGINEERING, INC.
CONSULTING ENGINEERS
111 JOHN STREET
NEW YORK, N.Y. 10038

KIRTI GANDHI, Ph.D., P.E.
PRESIDENT

SIGNATURE _____ DATE _____

TOPOGRAPHIC SURVEY PREPARED BY:
DRAWN BY: KK
CADD FILE:
Typical Details.dwg
August 11, 2026-7:35PM

LICENSED LAND SURVEYOR

SCALE
NOT TO SCALE


CITY OF NEW YORK
DEPARTMENT OF DESIGN + CONSTRUCTION
DIVISION OF INFRASTRUCTURE
BUREAU OF DESIGN

TYPICAL DETAILS - 3


NO.	DATE	DESCRIPTIONS REVISIONS	BY	APPR'D
VAN SINDEREN AVENUE STREETSCAPE IMPROVEMENTS BOROUGH OF BROOKLYN				
PROJECT ID: NDF-IBZ		DATE: 04/01/2019	SHEET 5 OF 22	D3 07

CONSULTANT DESIGN

PROJECT ID NDF-IBZ

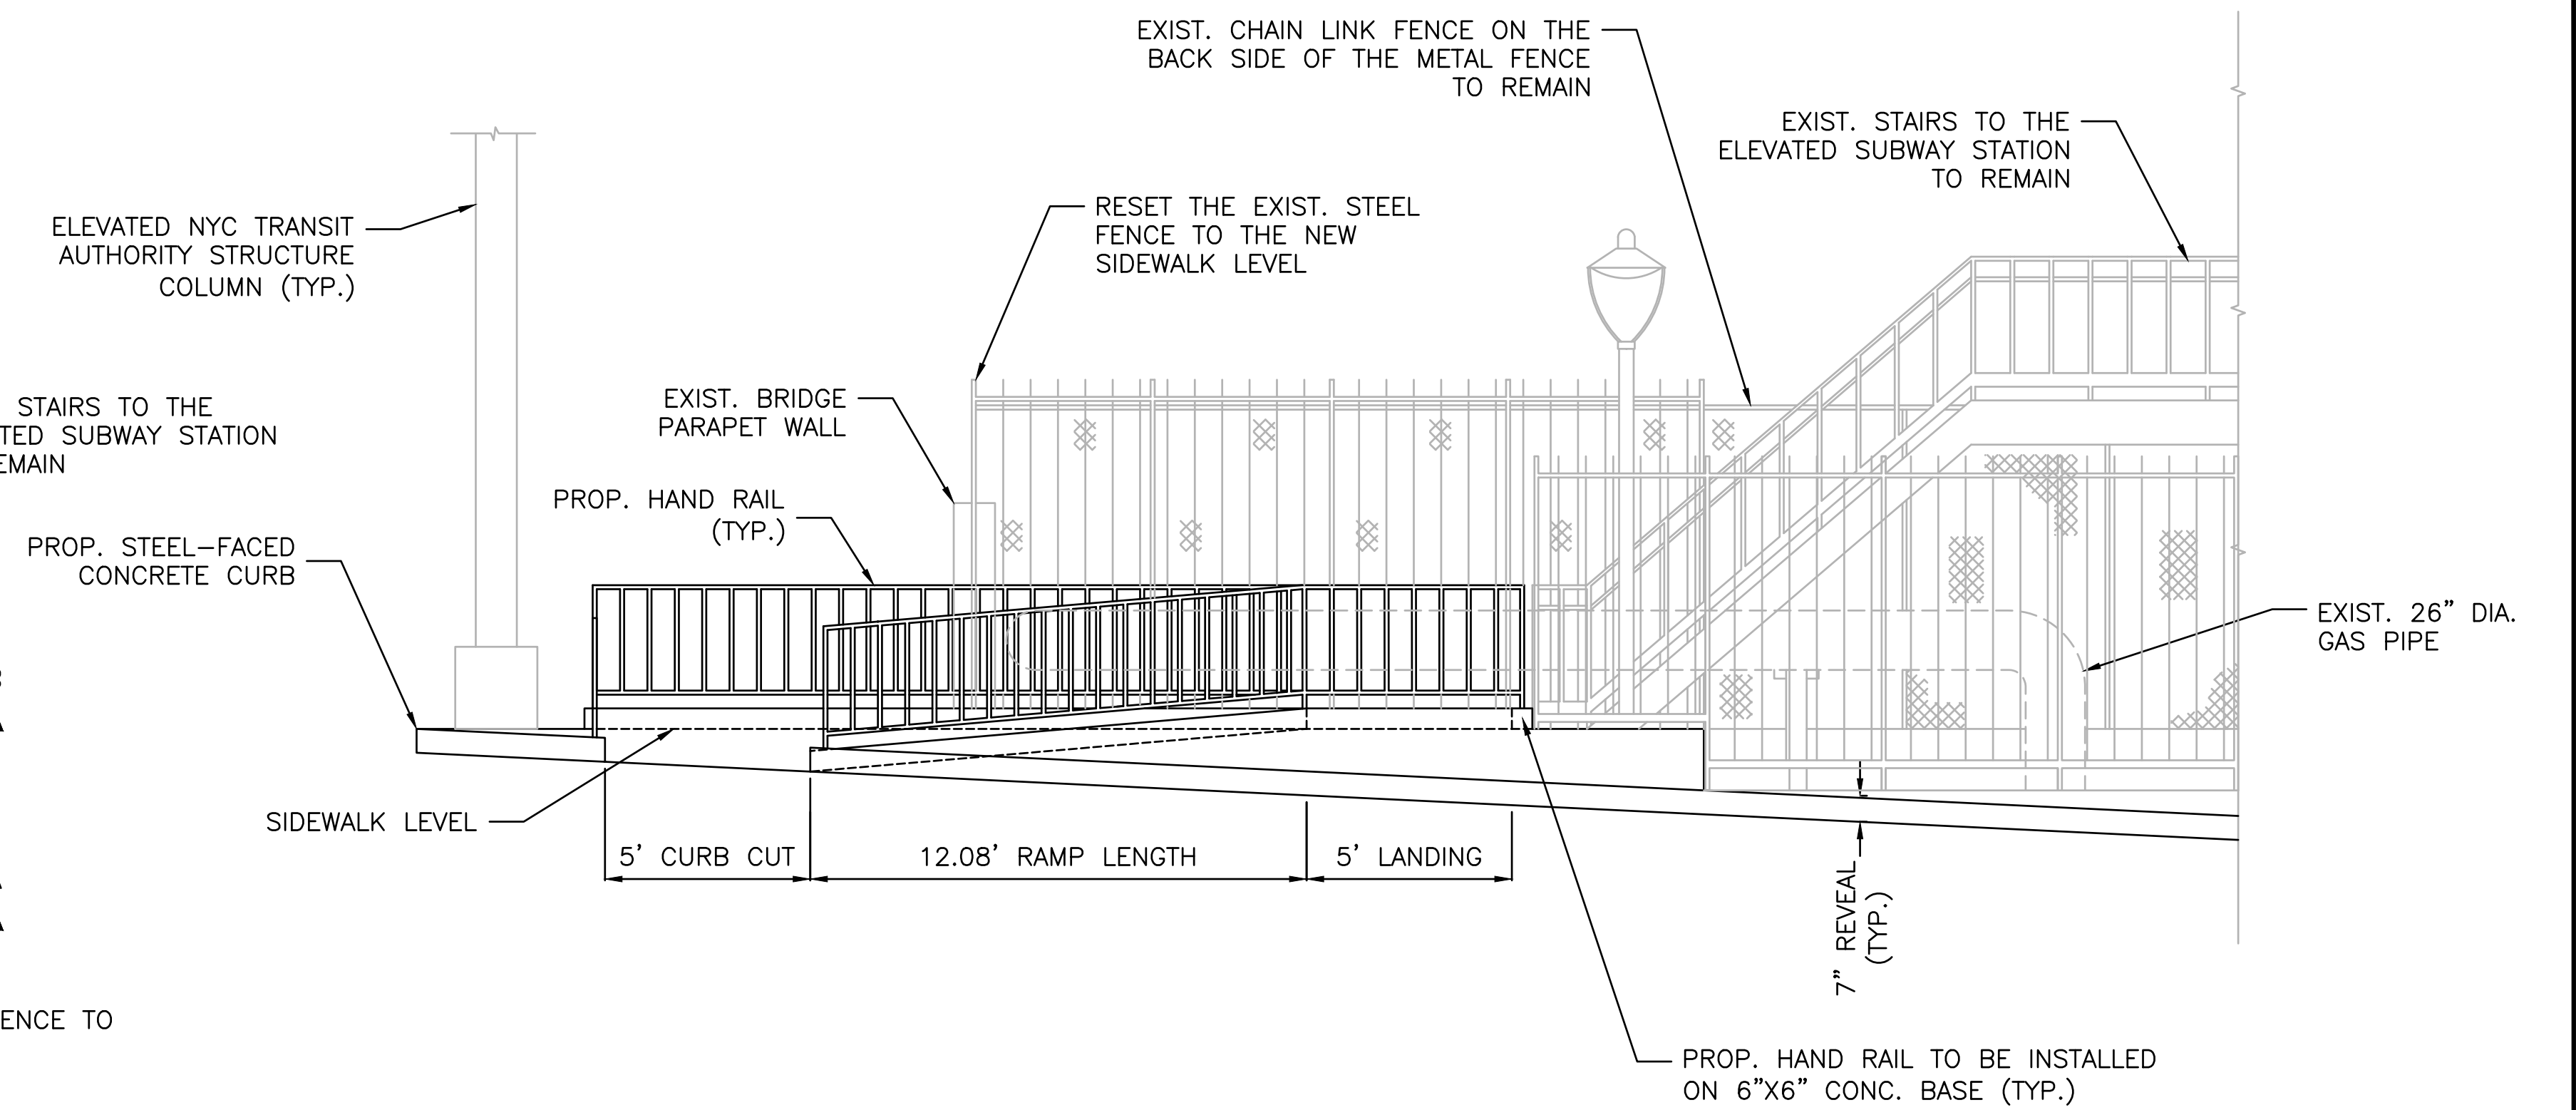


SECTION A-A

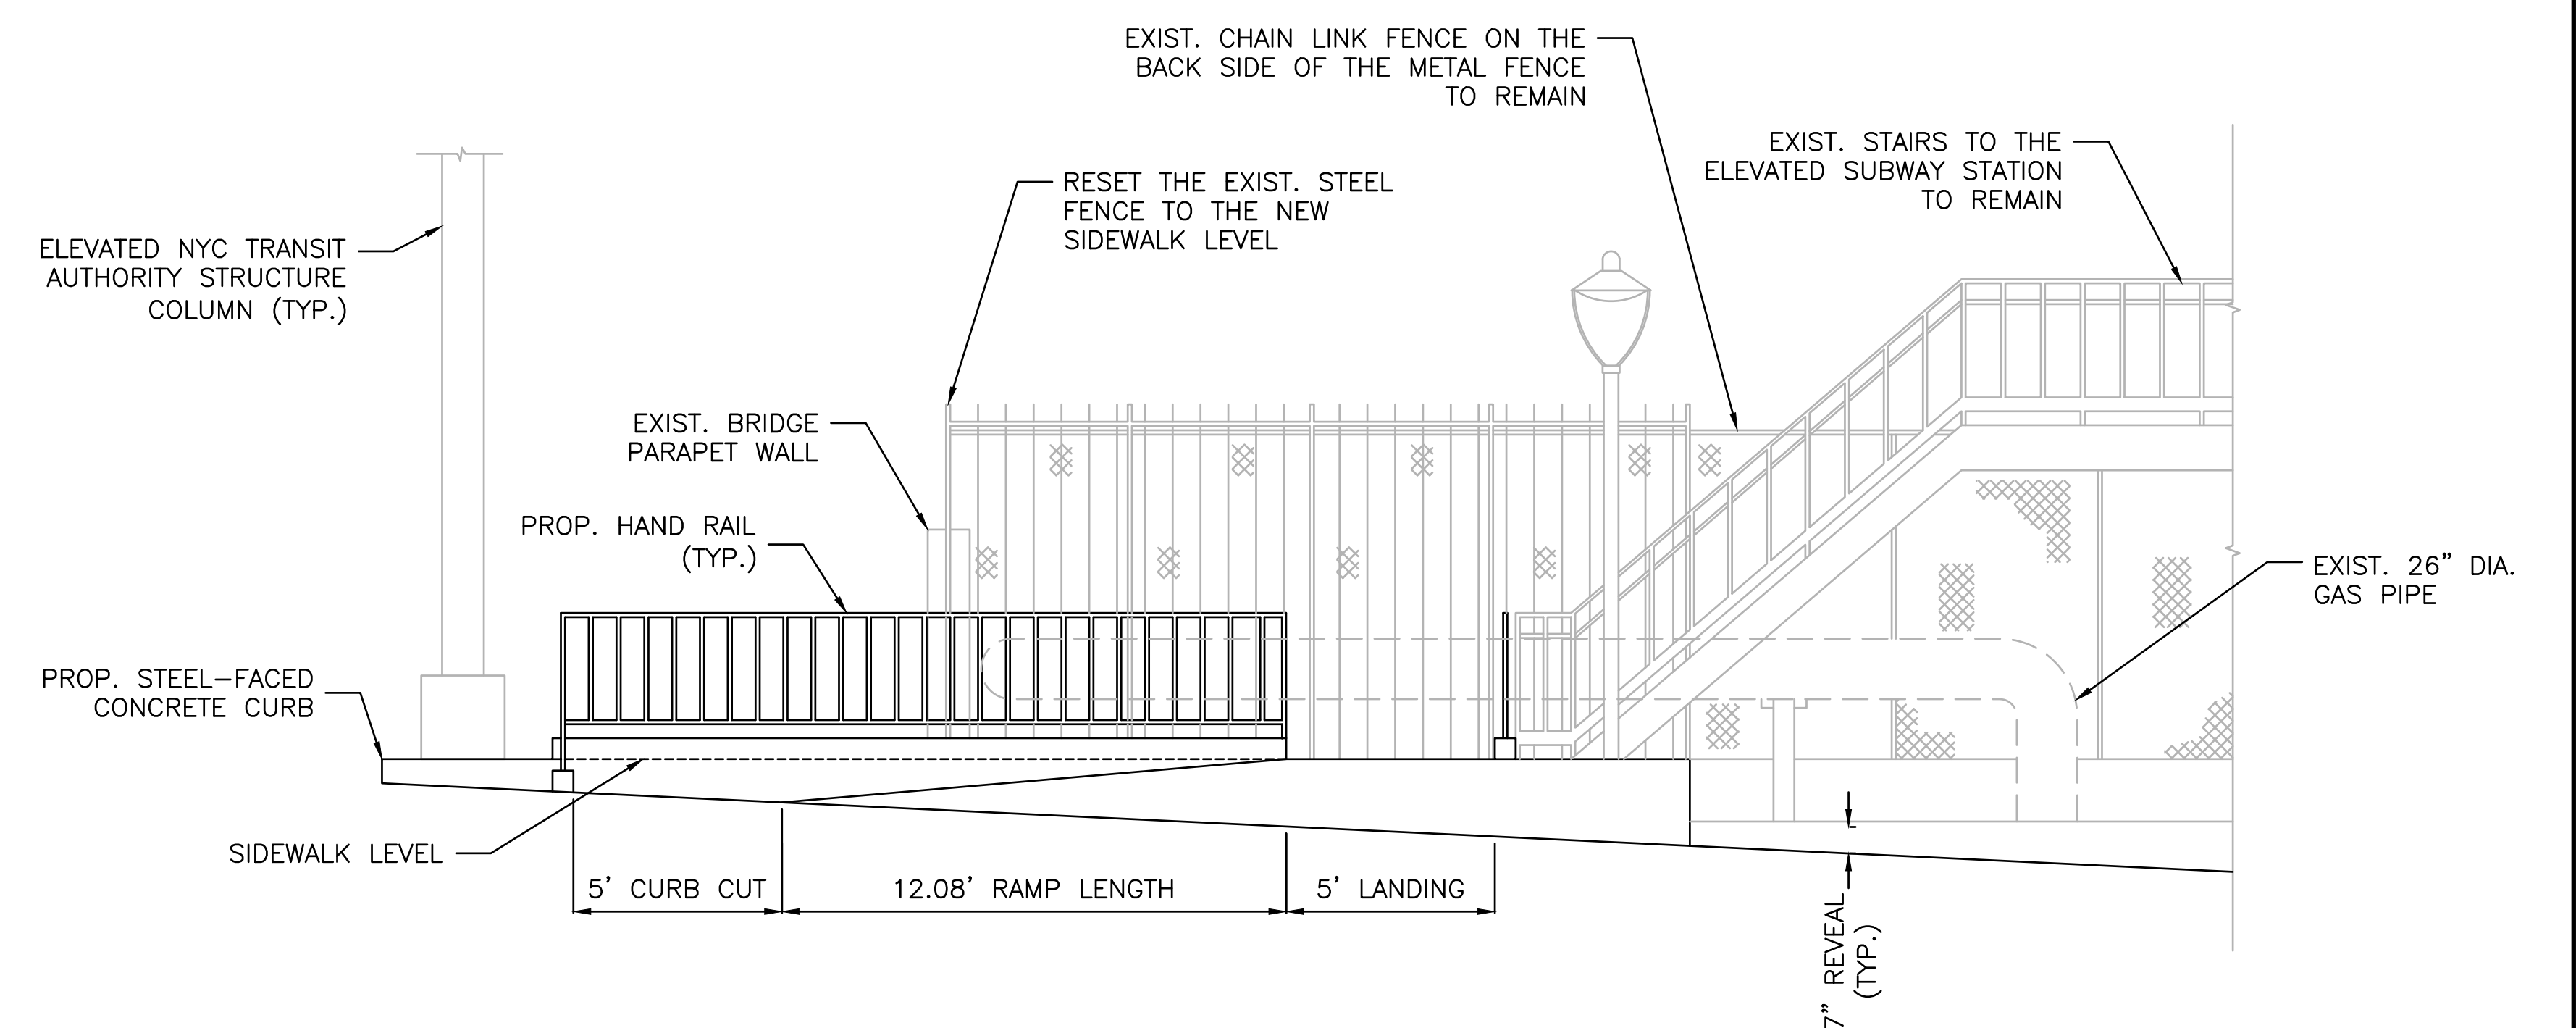


SECTION B-B

NO.	DATE	DESCRIPTIONS REVISIONS	BY	APPR'D
VAN SINDEREN AVENUE STREETSCAPE IMPROVEMENTS BOROUGH OF BROOKLYN				
PROJECT ID: NDF-IBZ		DATE: 04/01/2019	SHEET 6 OF 22	D4/D7

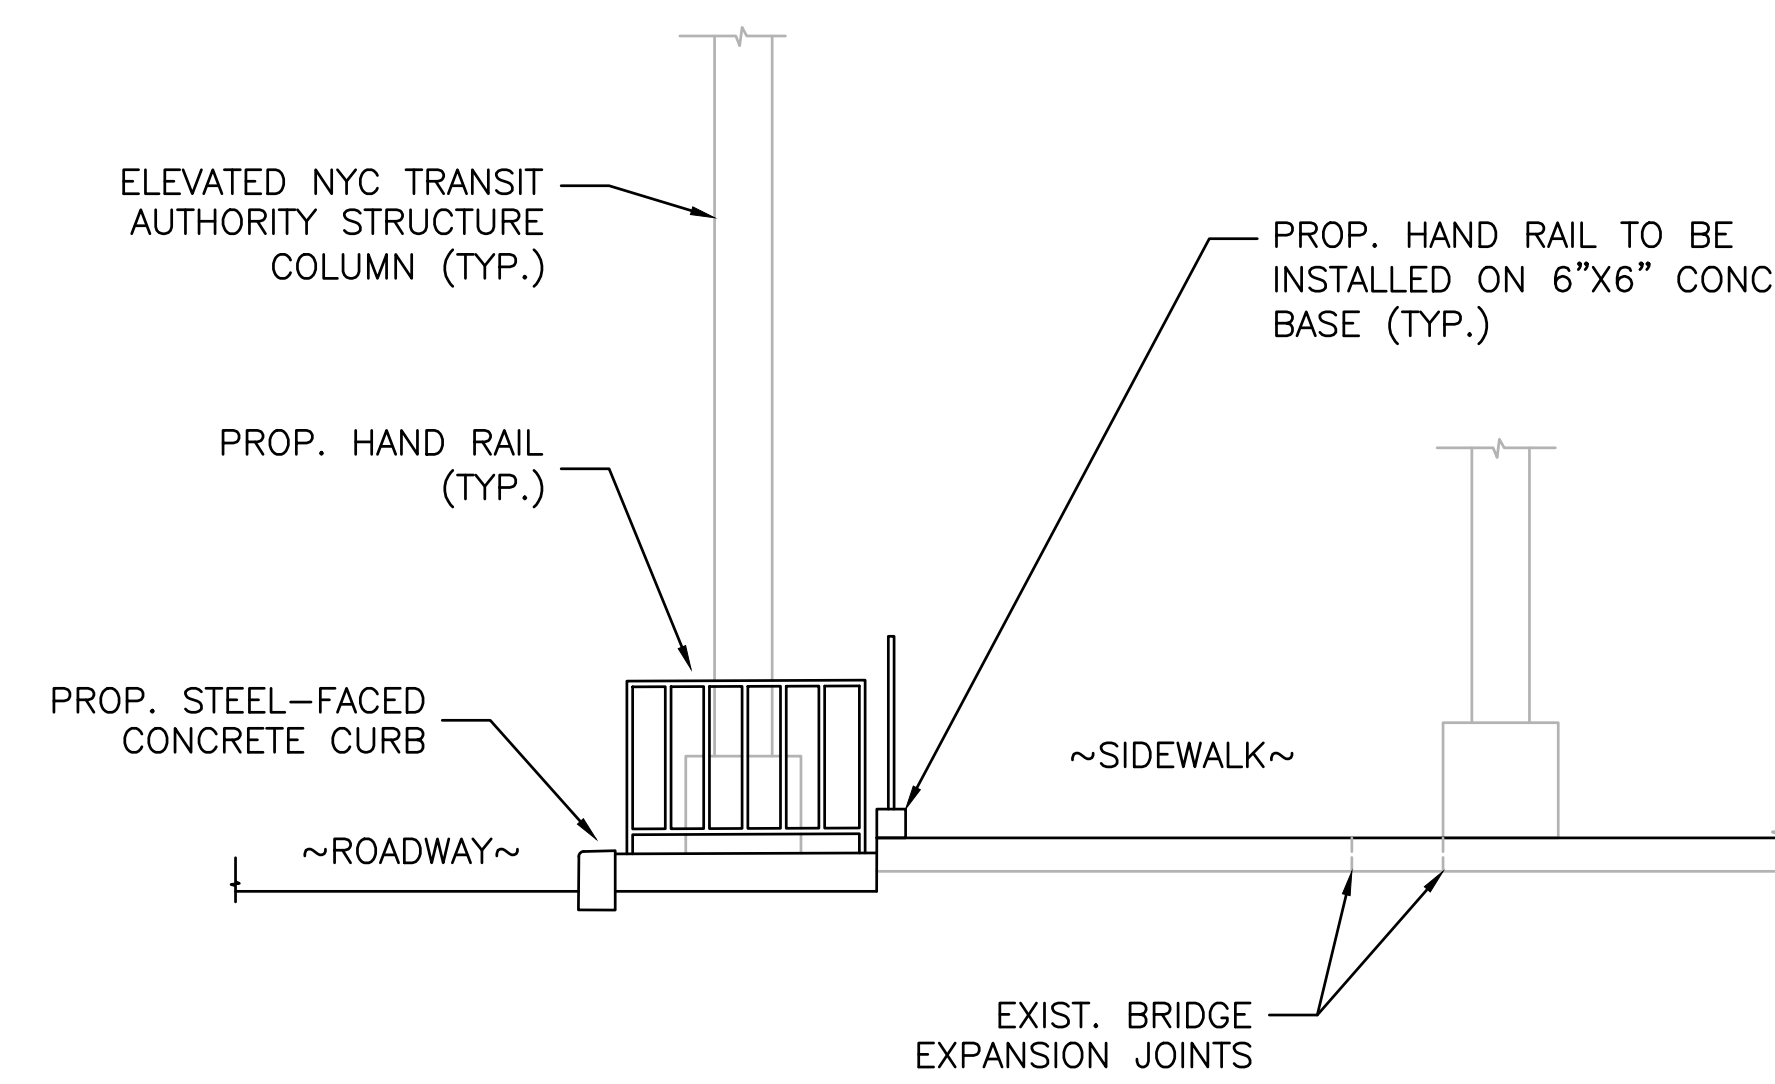

SECTION C-C



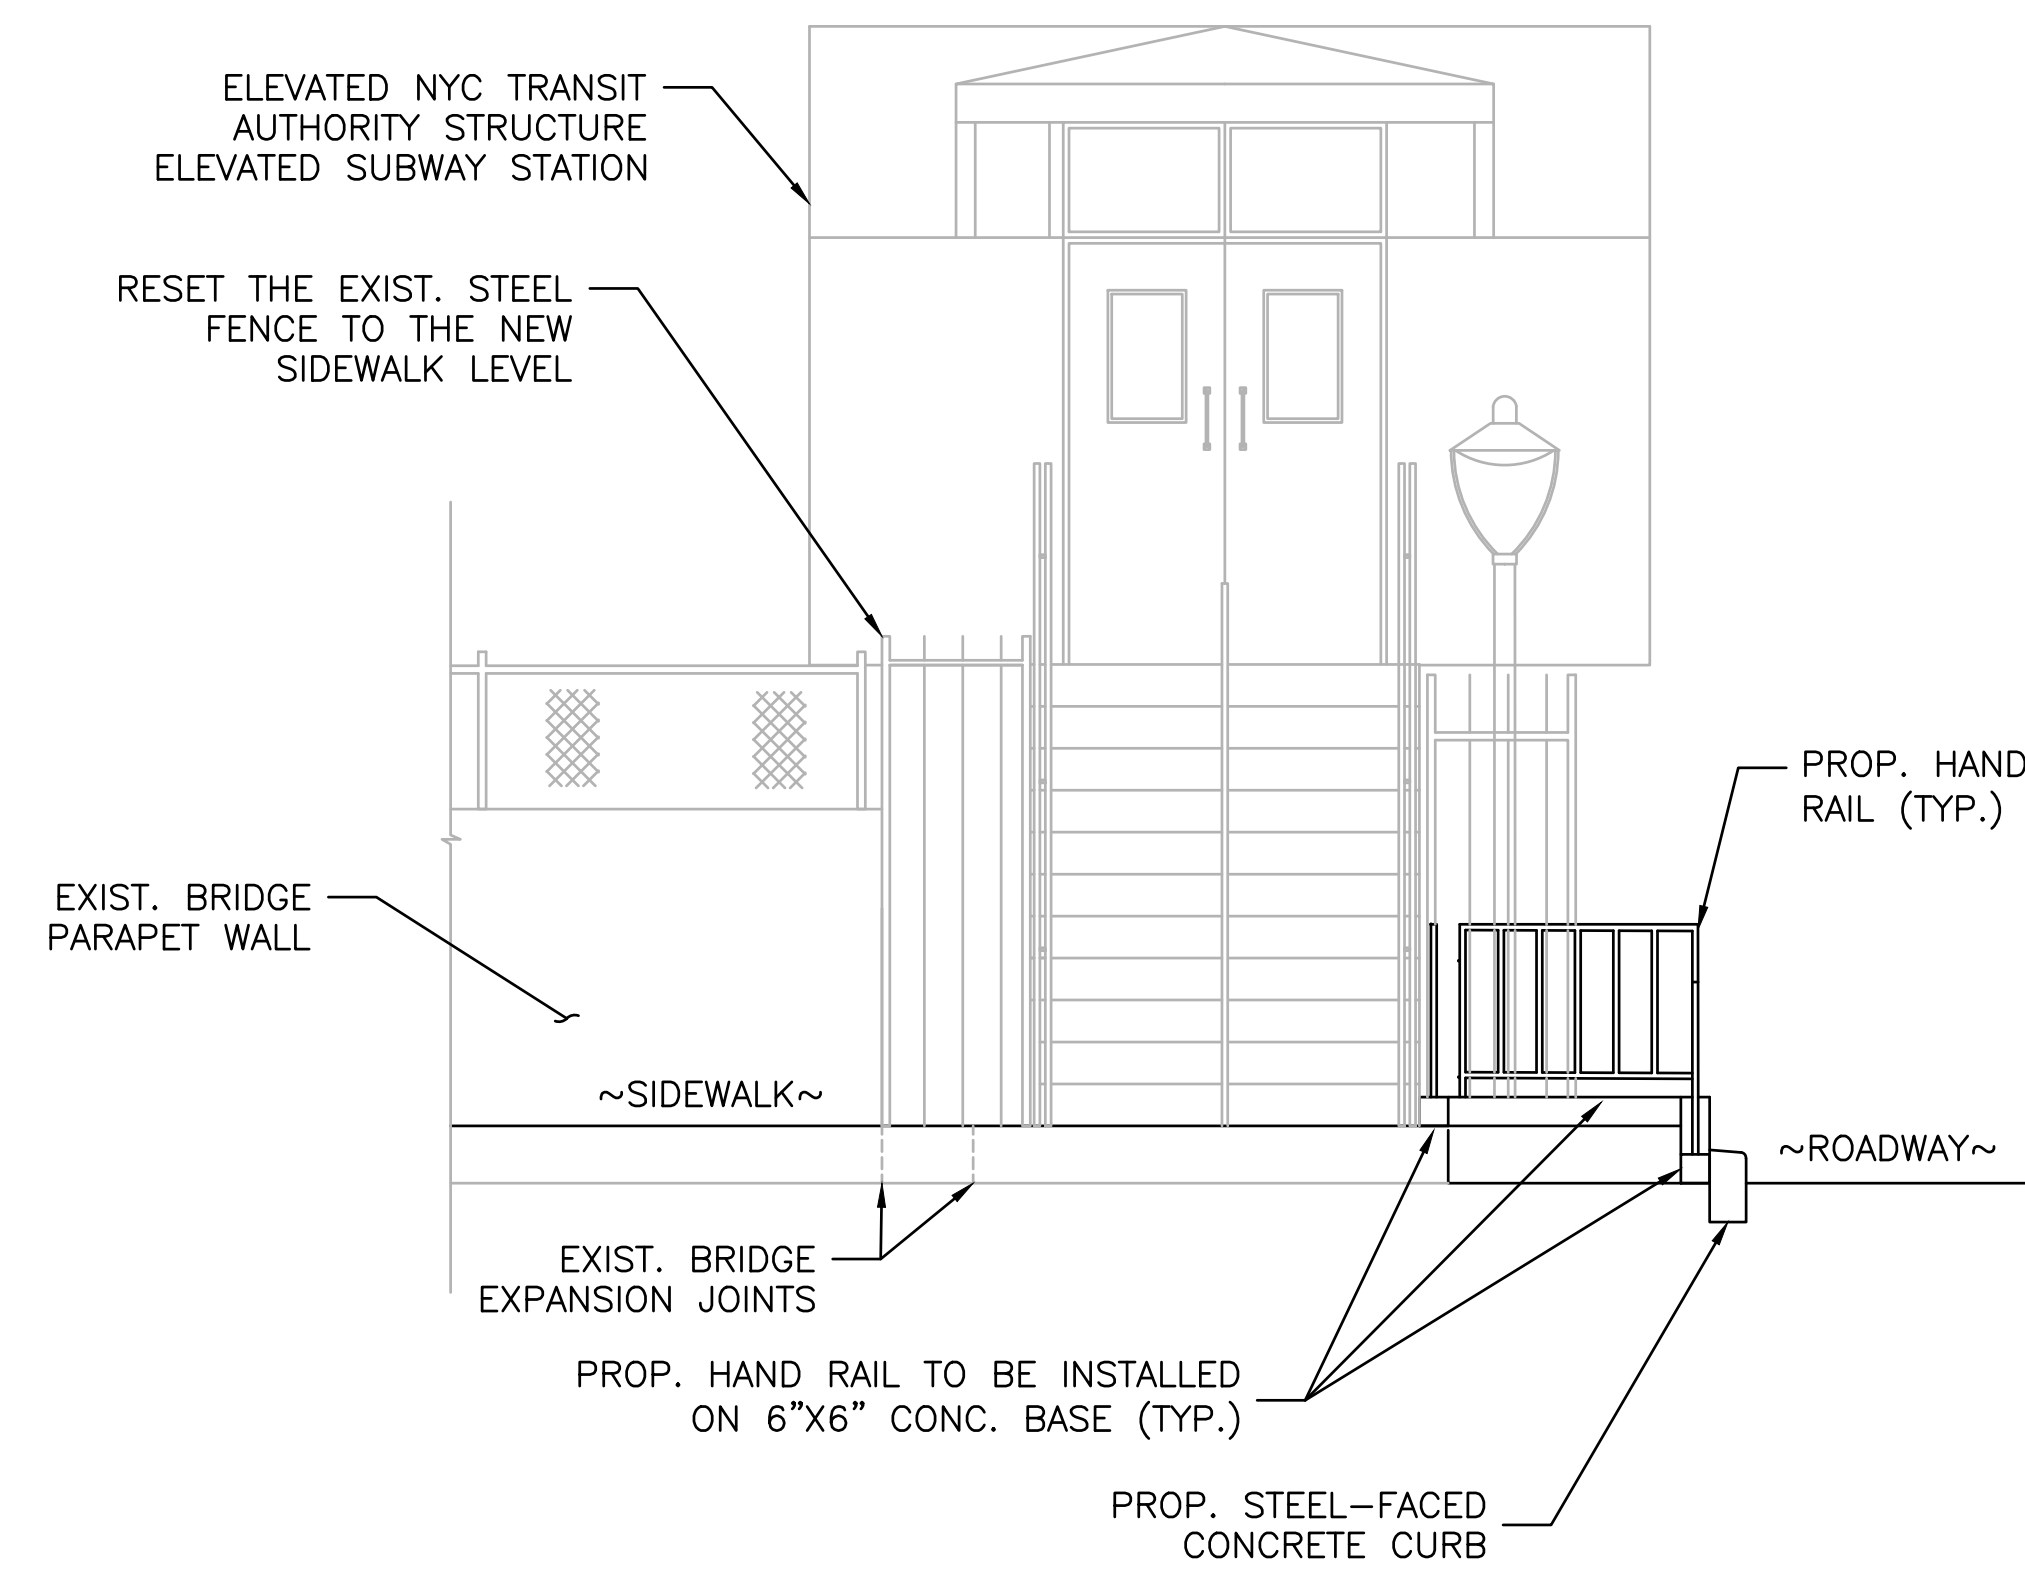


SECTION D-D

DETAIL #1
DESIGN OPTION A:
PROPOSED IMPROVEMENTS AT VAN SINDEREN AVENUE
AND SUTTER AVENUE INTERSECTION (NW CORNER)
SCALE: N.T.S.

PROJECT ID NDF-IBZ

NO.	DATE	DESCRIPTIONS REVISIONS	BY	APPR'D
VAN SINDEREN AVENUE				
STREETSCAPE IMPROVEMENTS				
BOROUGH OF BROOKLYN				
PROJECT ID: NDF-IBZ		DATE: 04/01/2019	SHEET 7 OF 22	D5 / 57

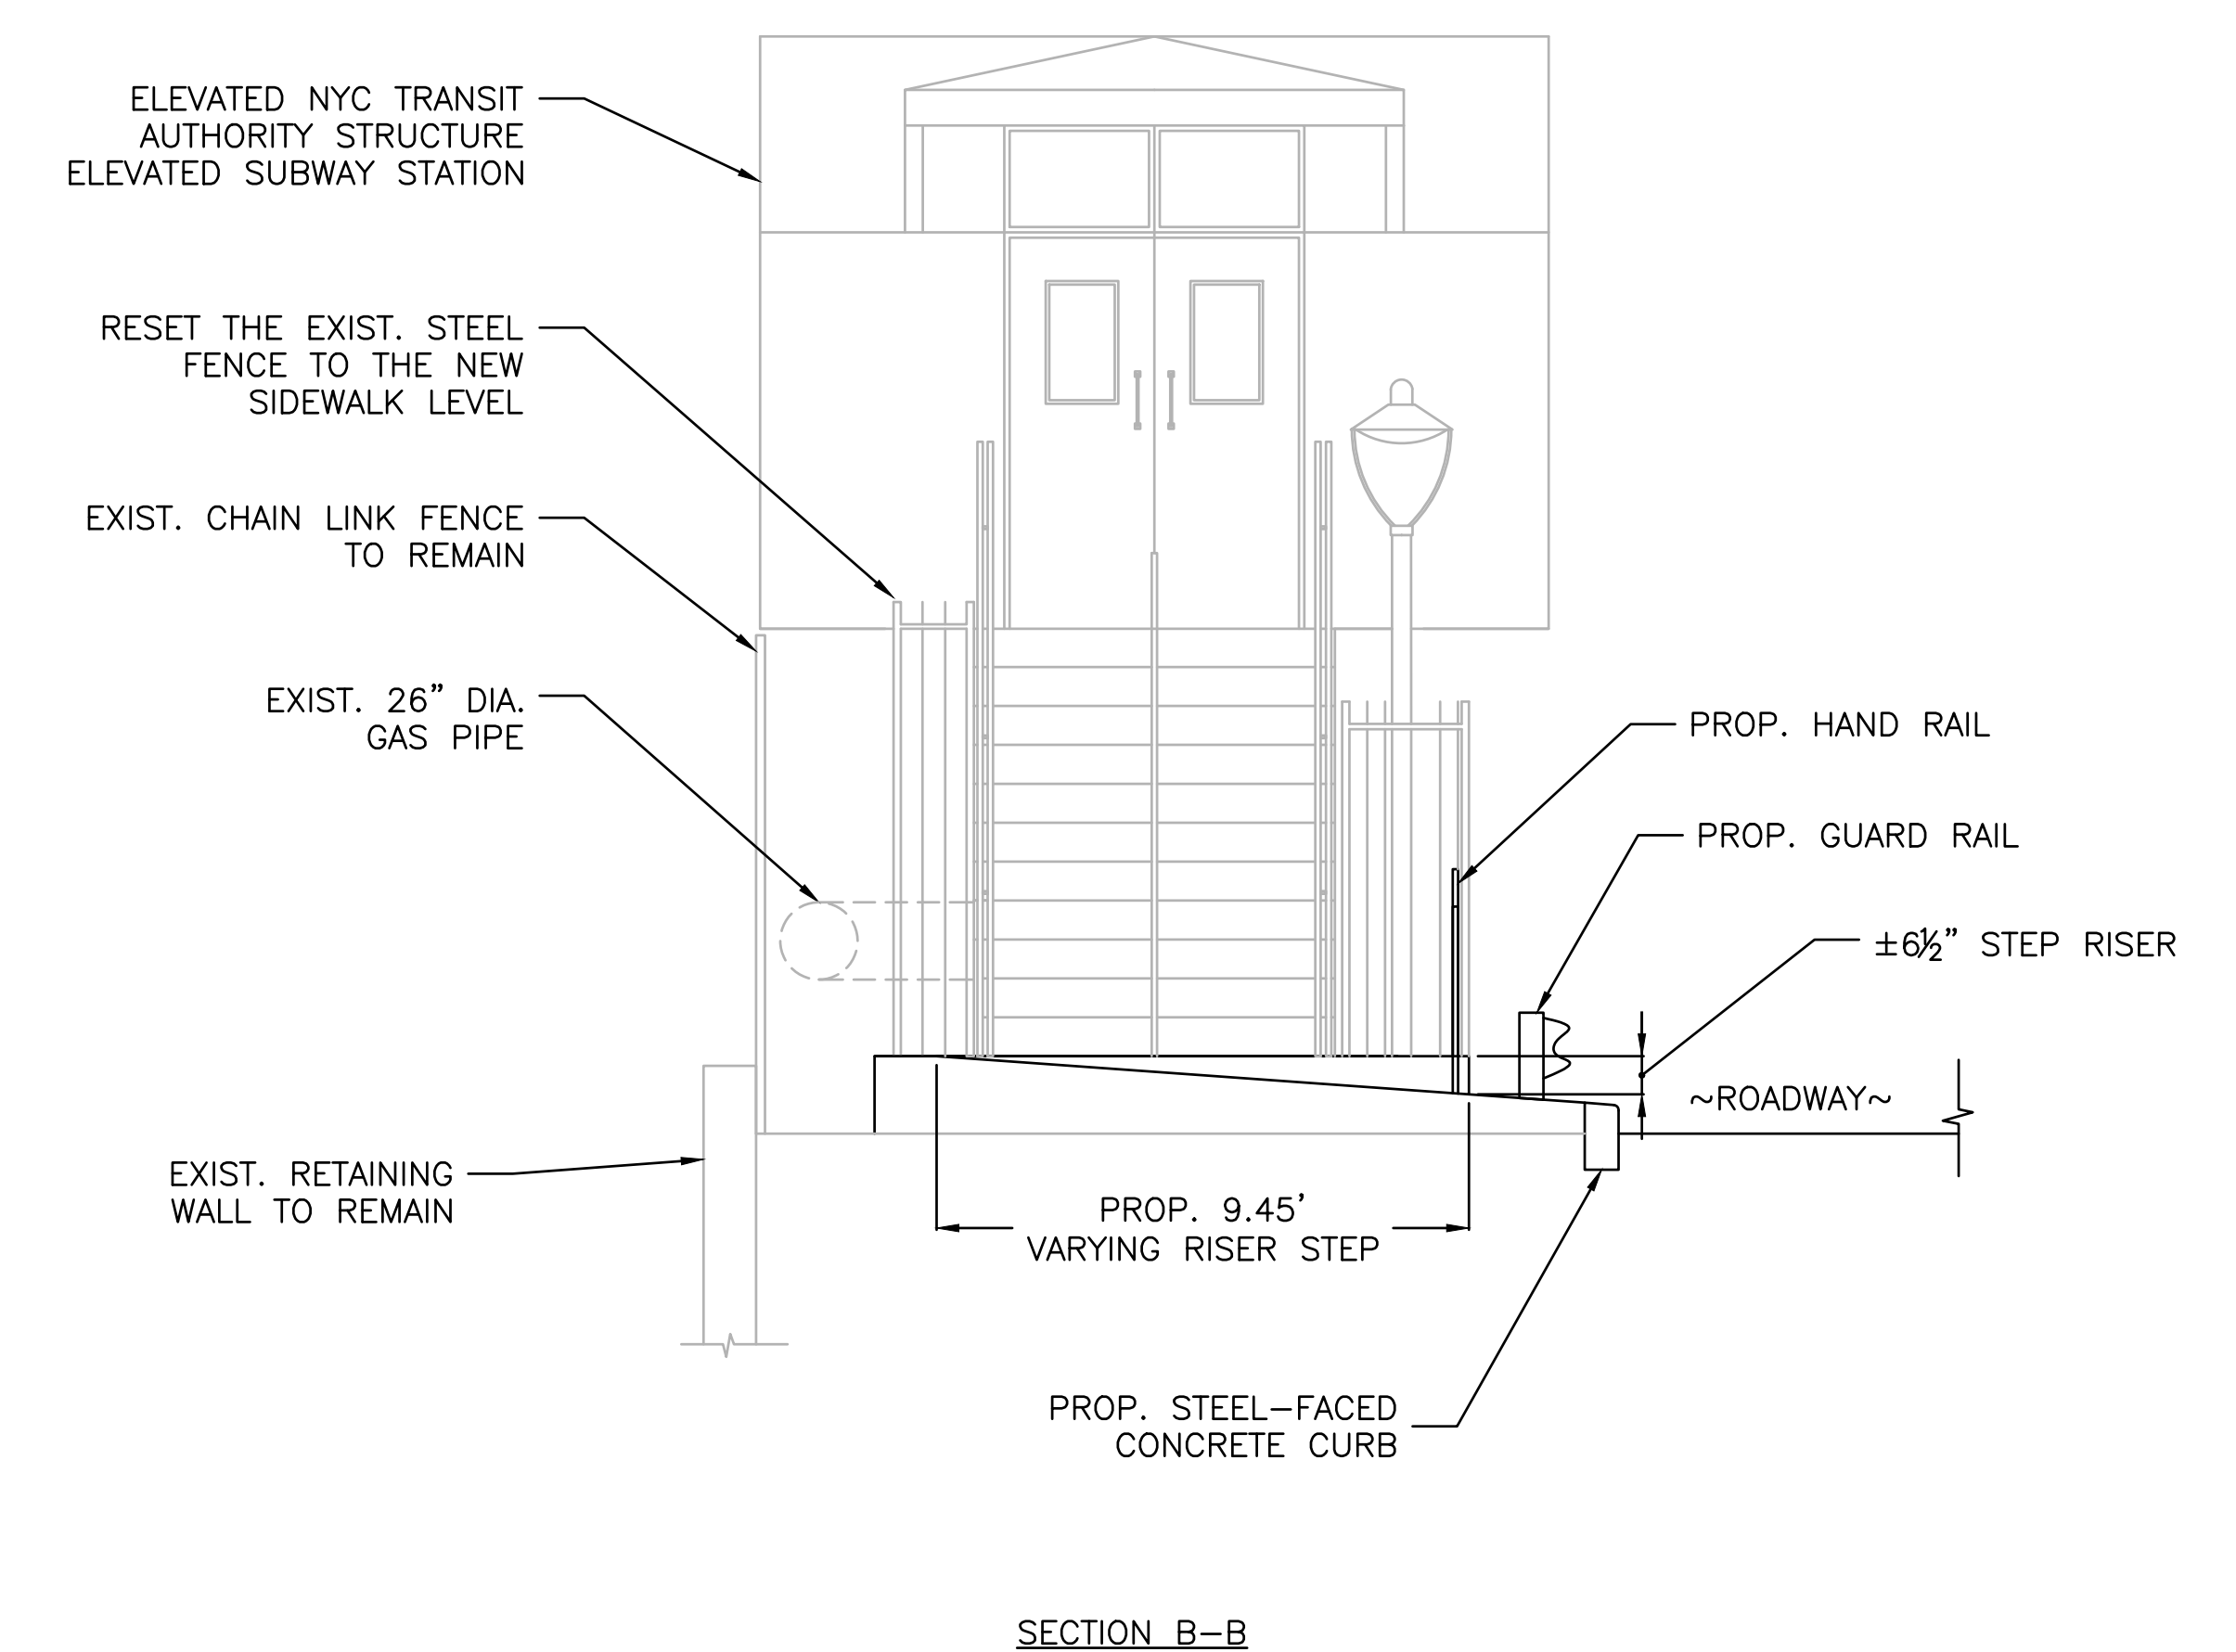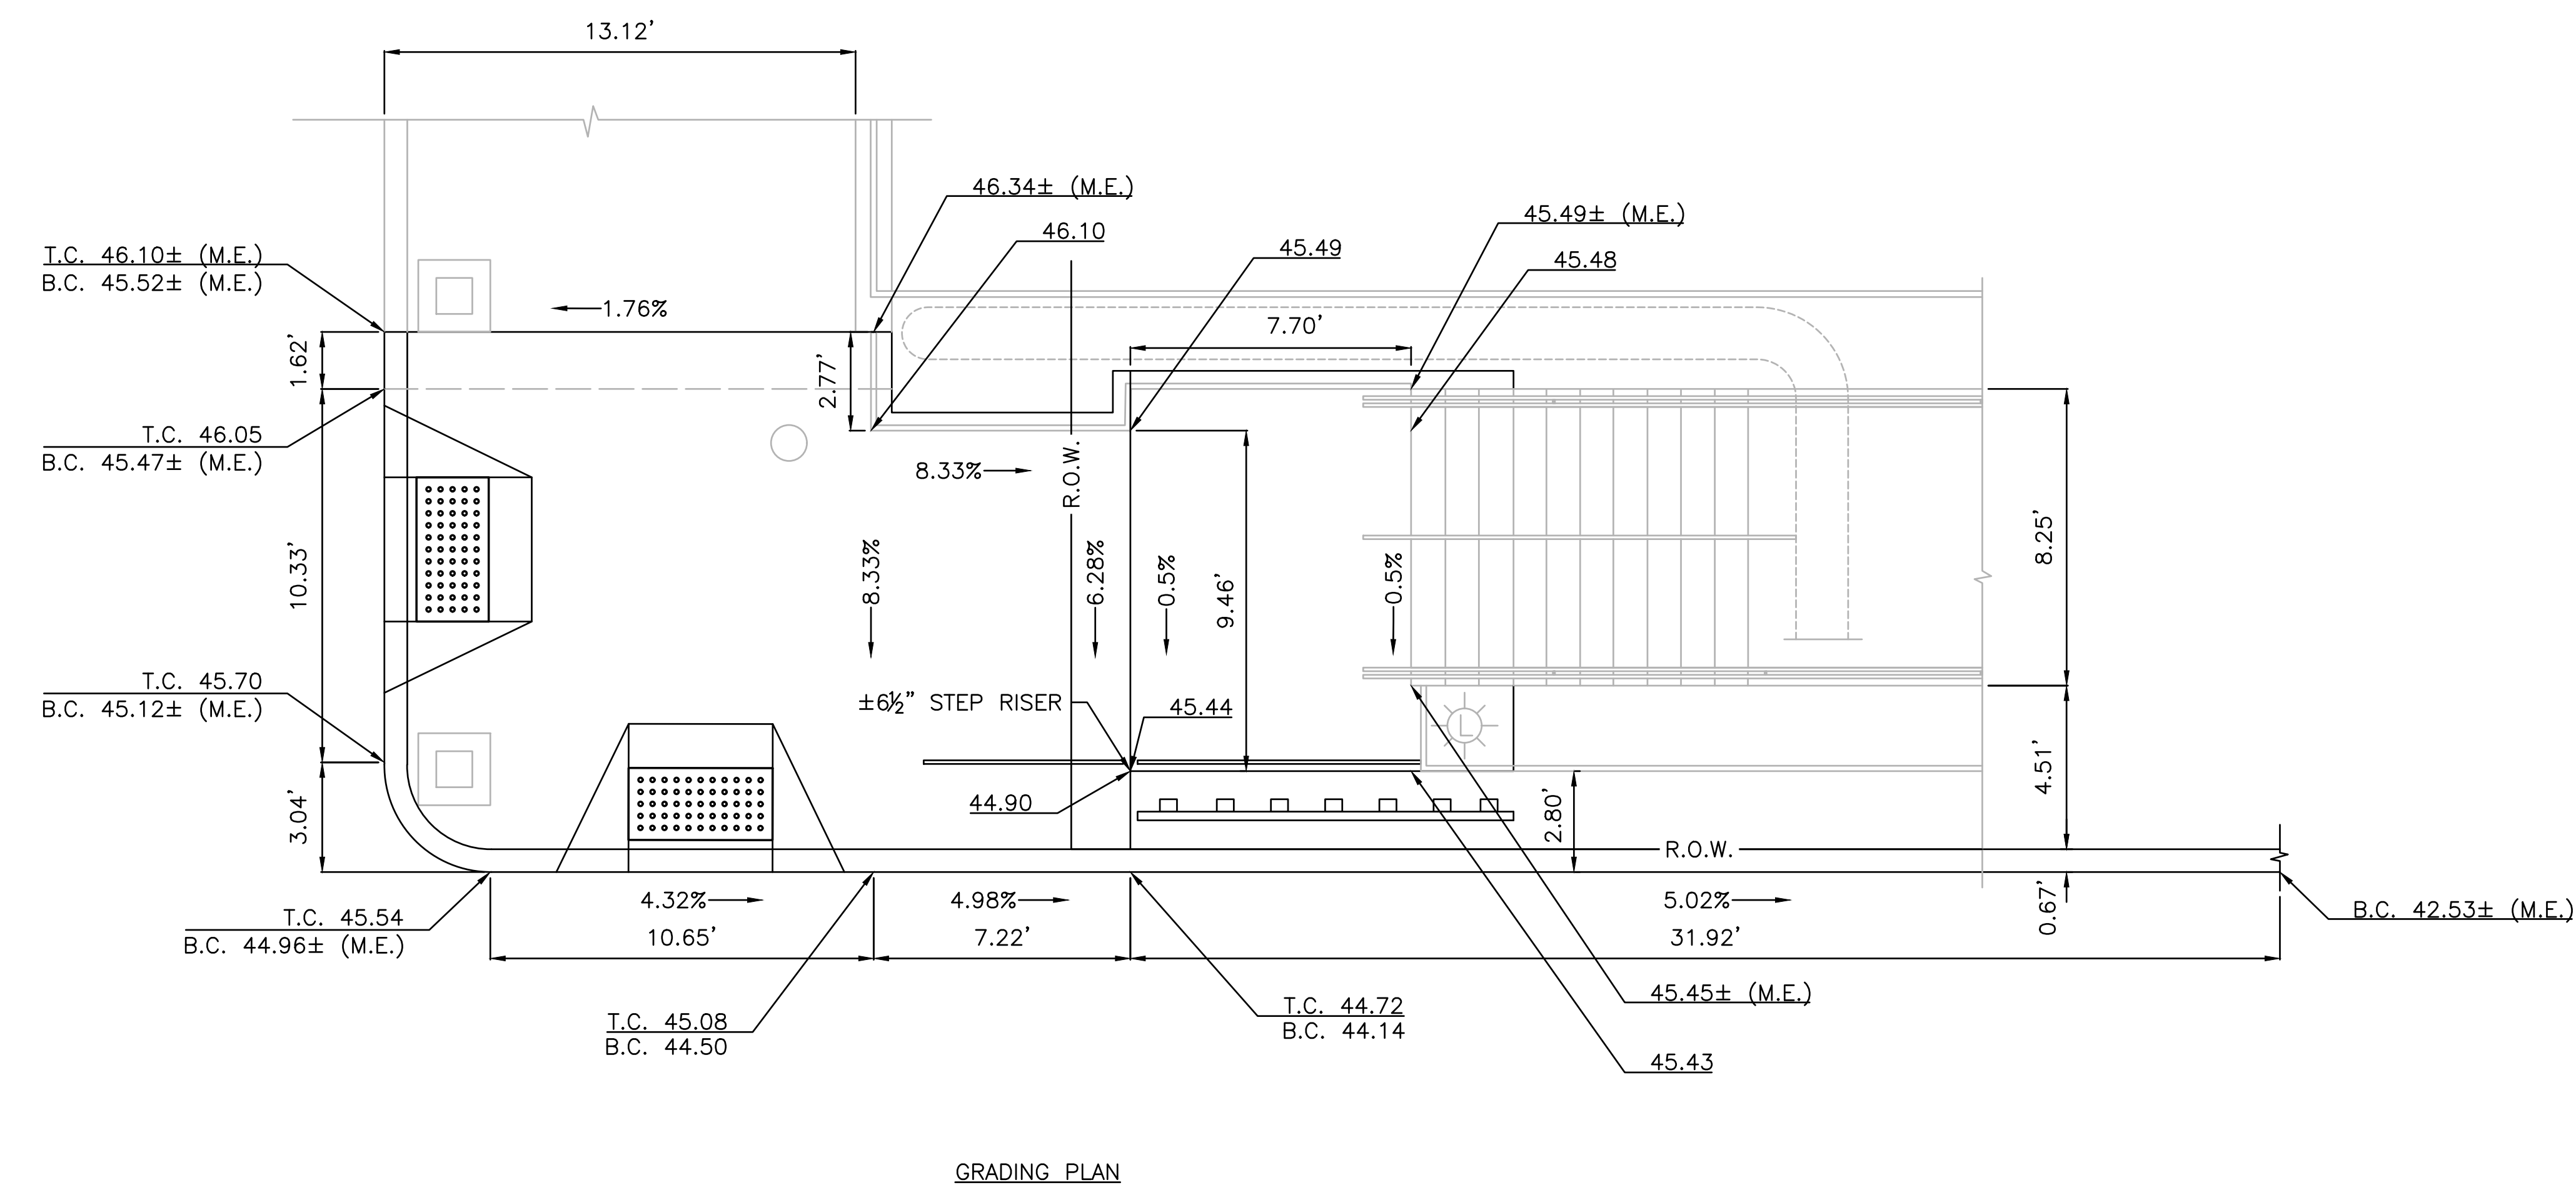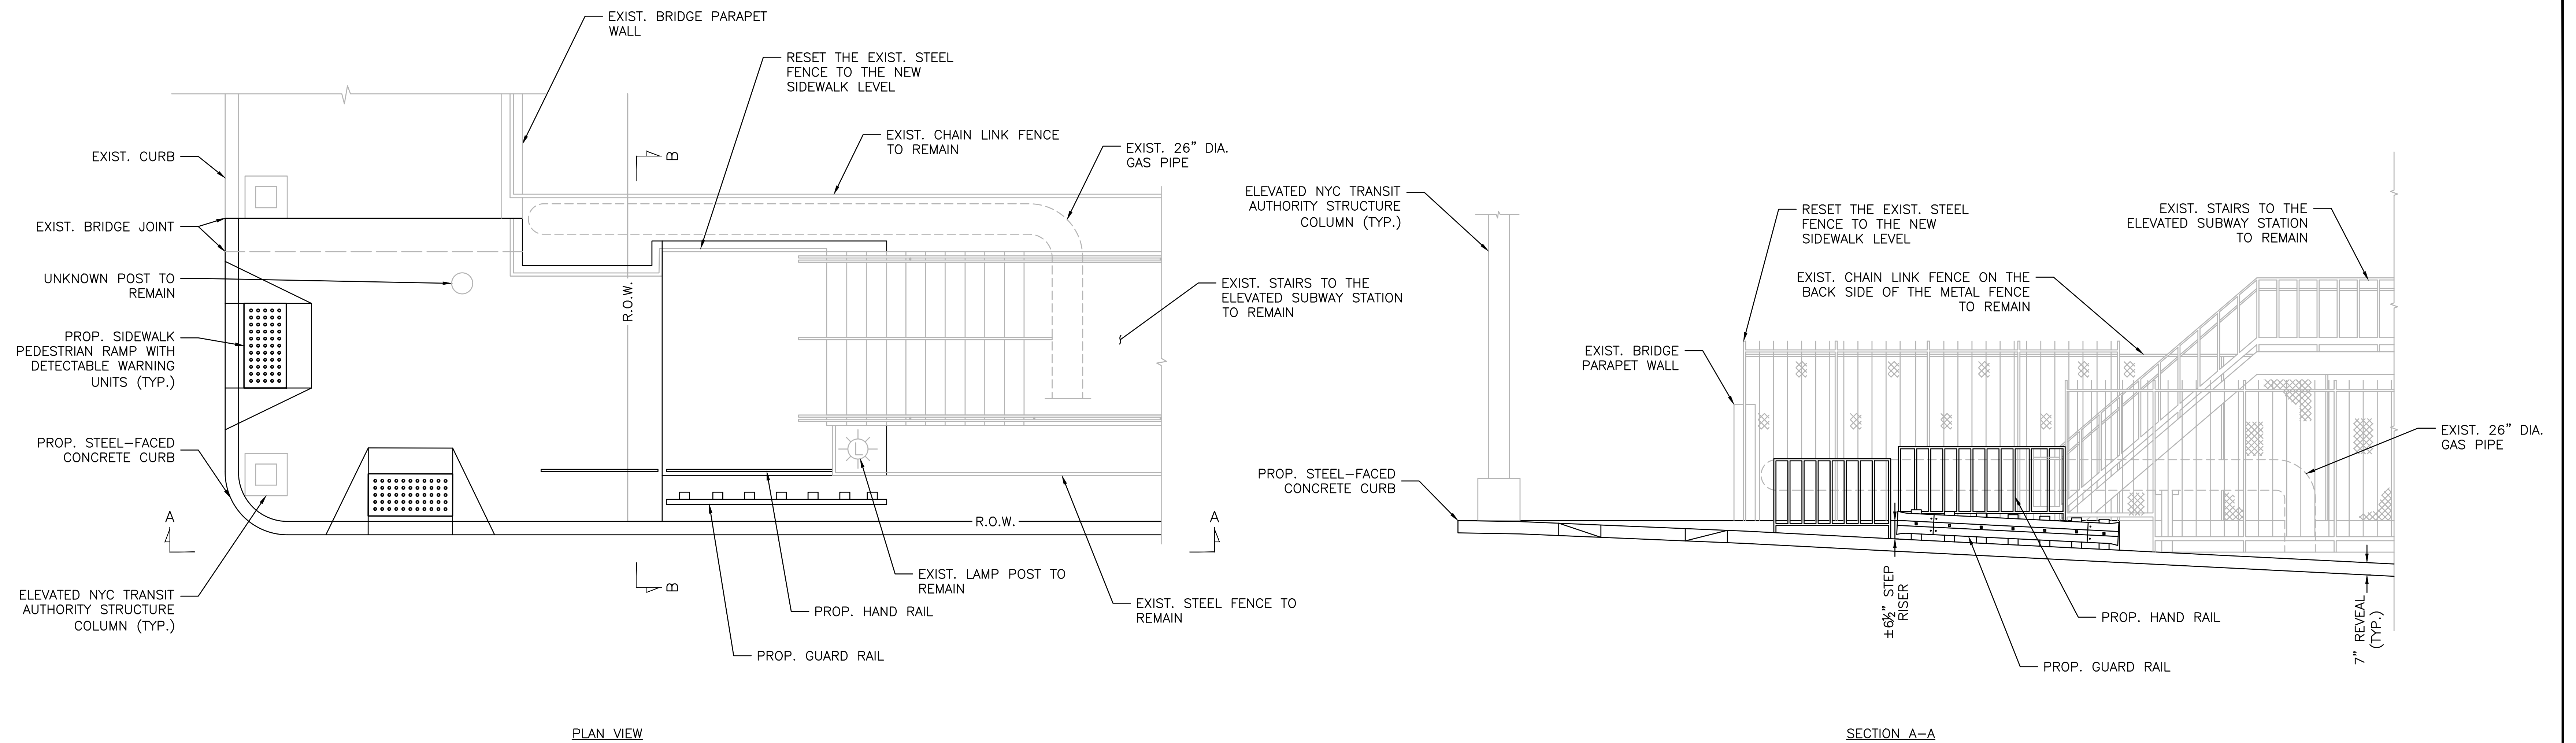

DETAIL #1
DESIGN OPTION B:
PROPOSED IMPROVEMENTS AT VAN SINDEREN AVENUE
AND SUTTER AVENUE INTERSECTION (NW CORNER)
SCALE: N.T.S.

NO.	DATE	DESCRIPTIONS REVISIONS		BY	APPR'D
VAN SINDEREN AVENUE STREETSCAPE IMPROVEMENTS BOROUGH OF BROOKLYN					
PROJECT ID: NDF-IBZ		DATE: 04/01/2019		SHEET 8	OF 22
					D\$ 07

FINAL DESIGN PREPARED BY: KIRTI GANDHI, Ph.D., P.E.
PRESIDENT

 GANDHI ENGINEERING, INC.
CONSULTING ENGINEERS
111 JOHN STREET,
NEW YORK, N.Y. 10038

SIGNATURE _____

TOPOGRAPHIC SURVEY PREPARED BY:

LICENSED LAND SURVEYOR

DRAWN BY: KK
CADD FILE:
H:\Pruchhof\Place\New folder\W
Typical Details.dwg
August 11, 2026-7:3




SCALE

CITY OF NEW YORK
DEPARTMENT OF DESIGN + CONSTRUCTION
DIVISION OF INFRASTRUCTURE
BUREAU OF DESIGN

TYPICAL DETAILS - 6

PROJECT ID: NDF-IBZ	DATE: 04/01/2019	SHEET 8 OF 22	D6 D7	BC
---------------------	------------------	---------------	----------	----

CONSULTANT DESIGN

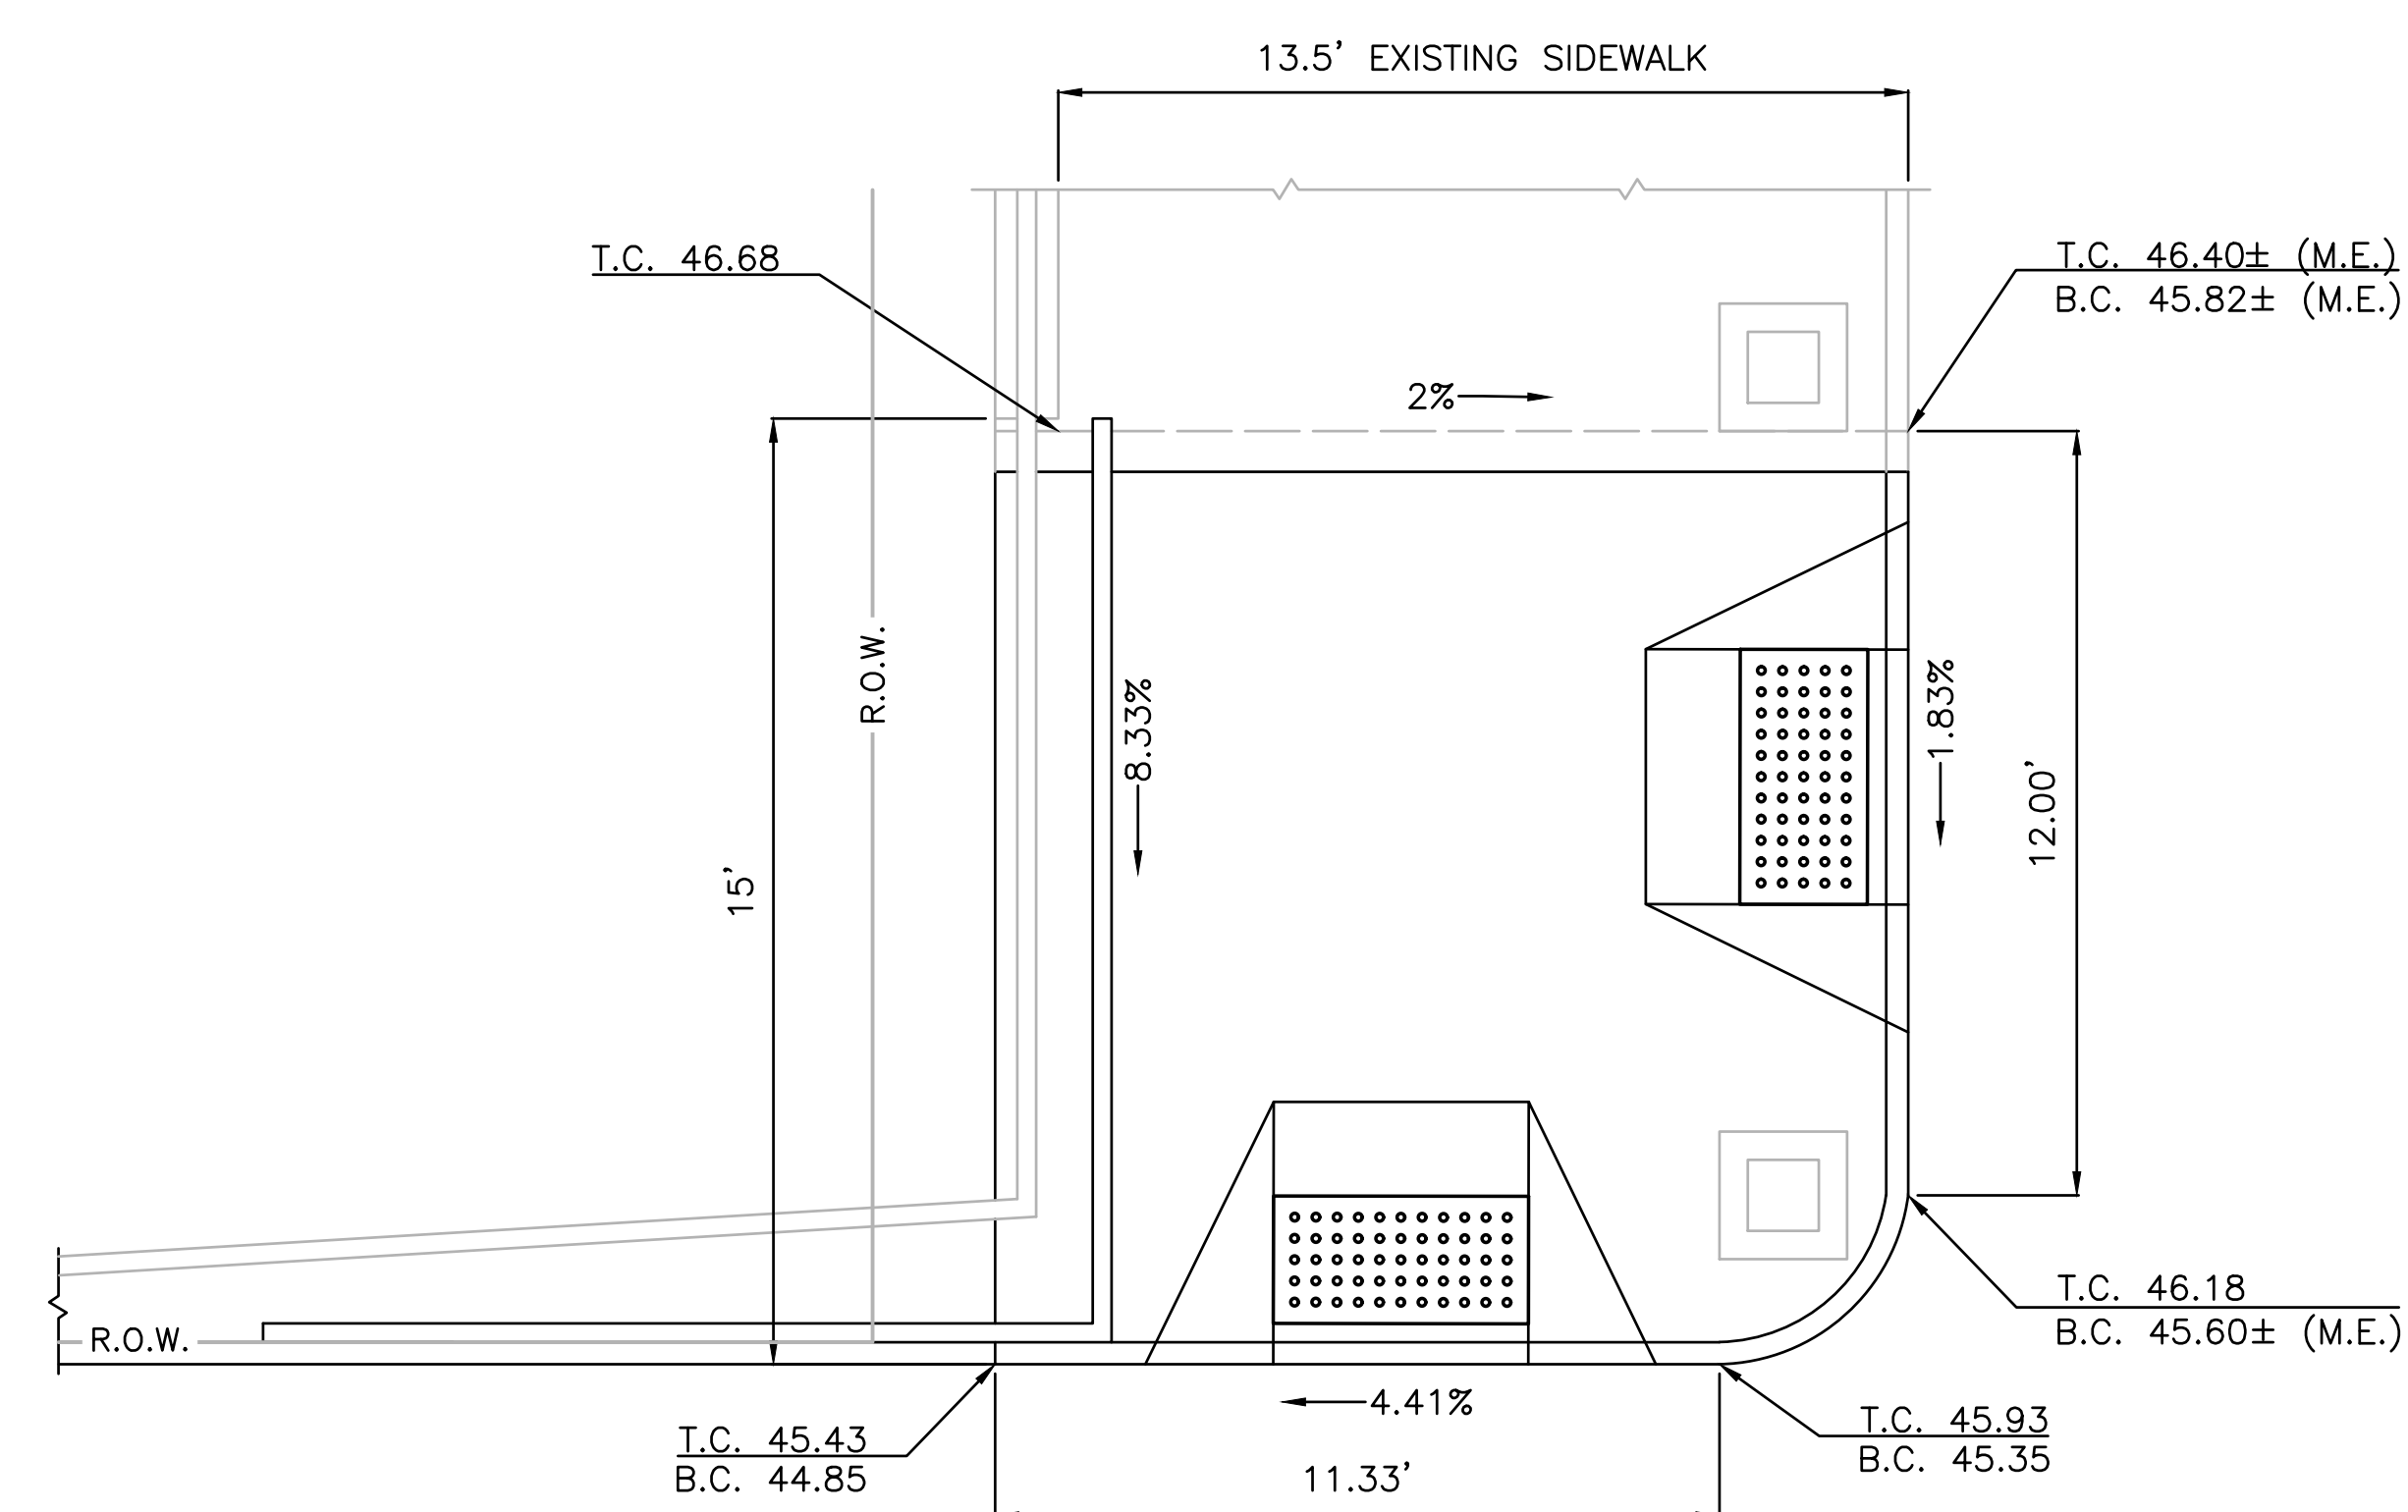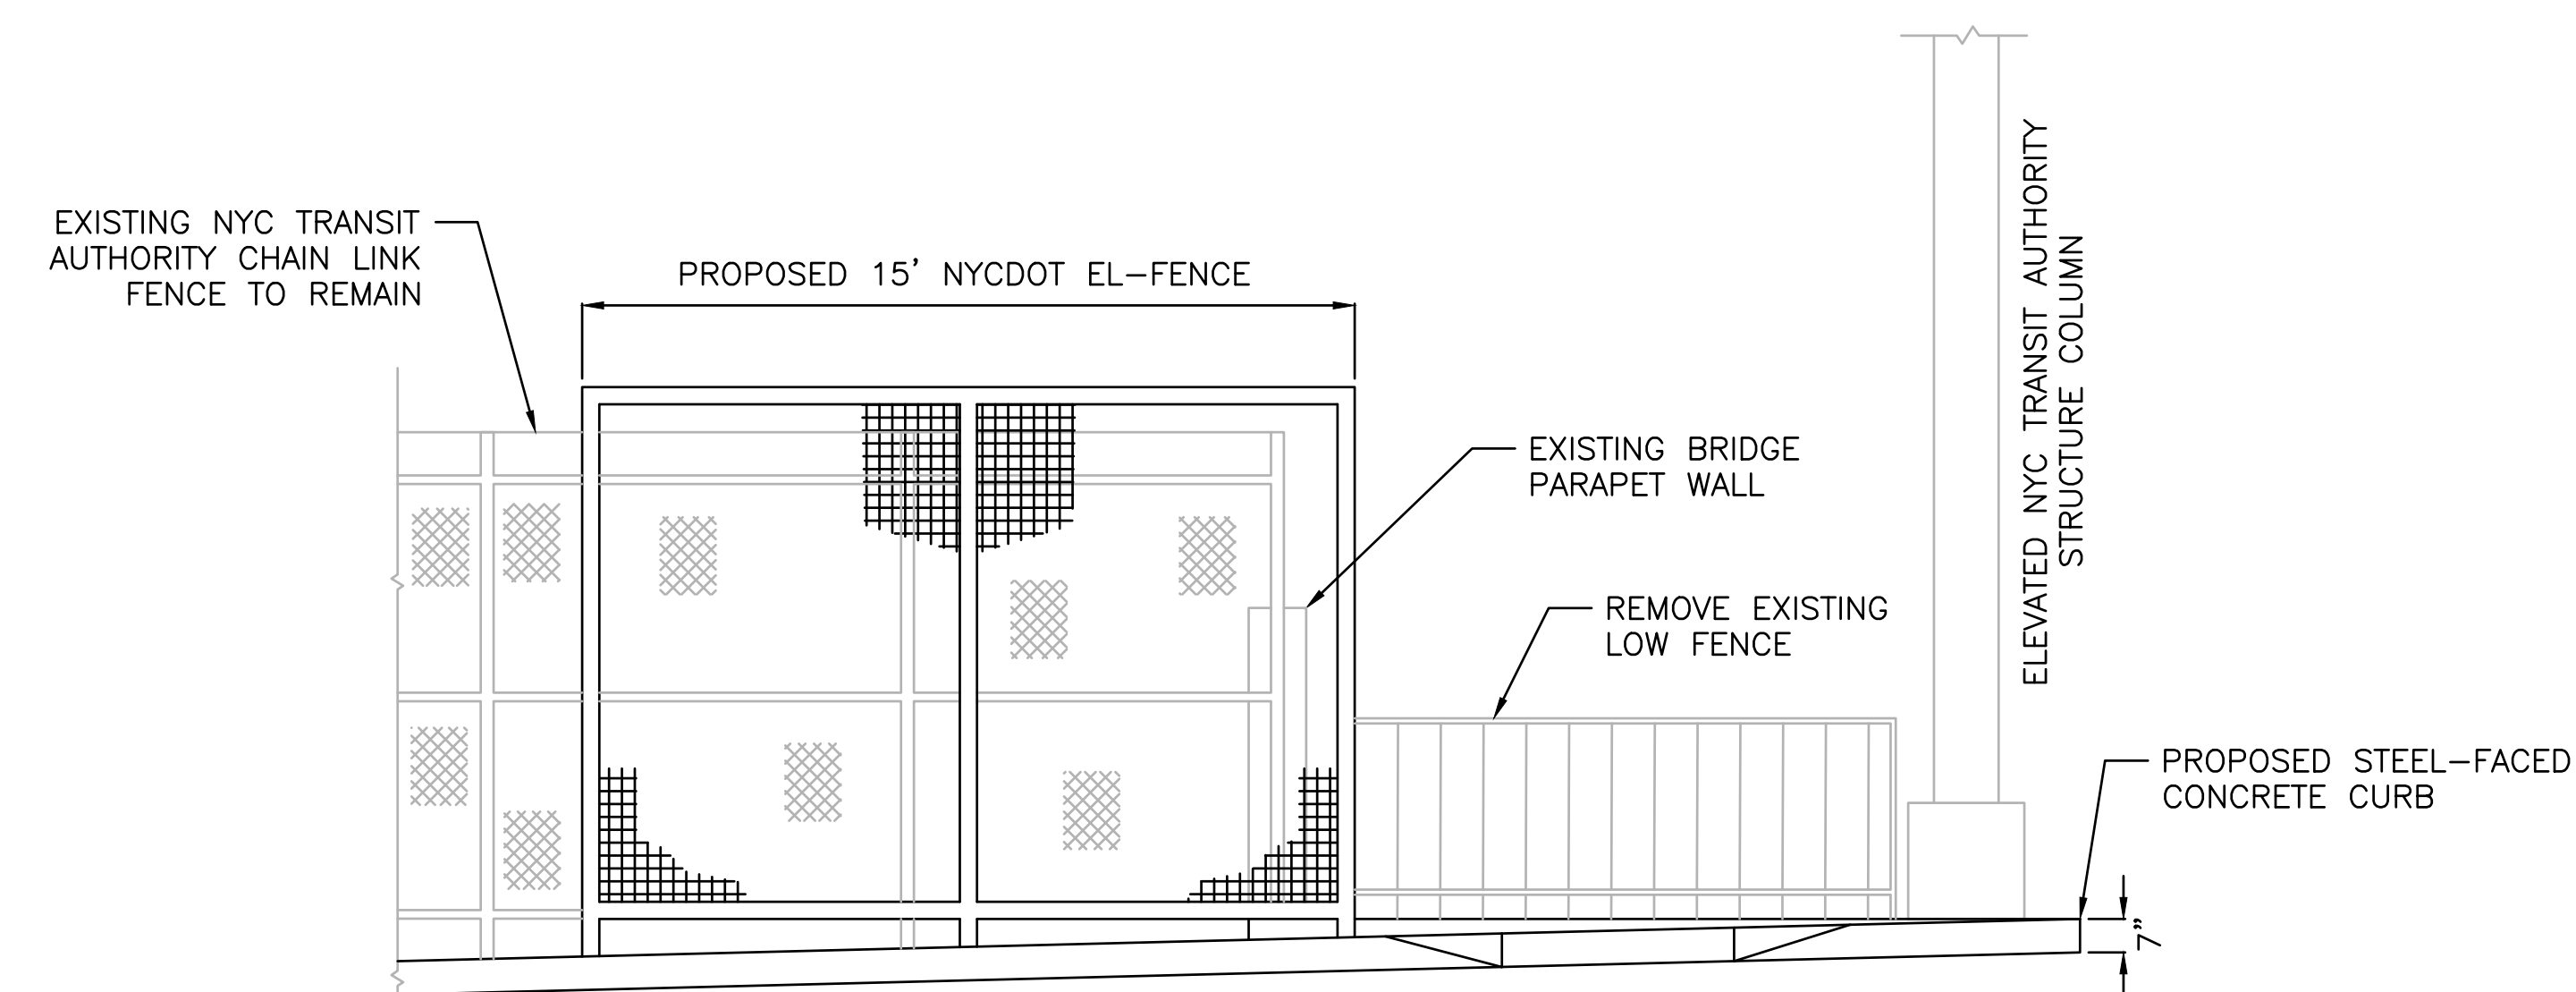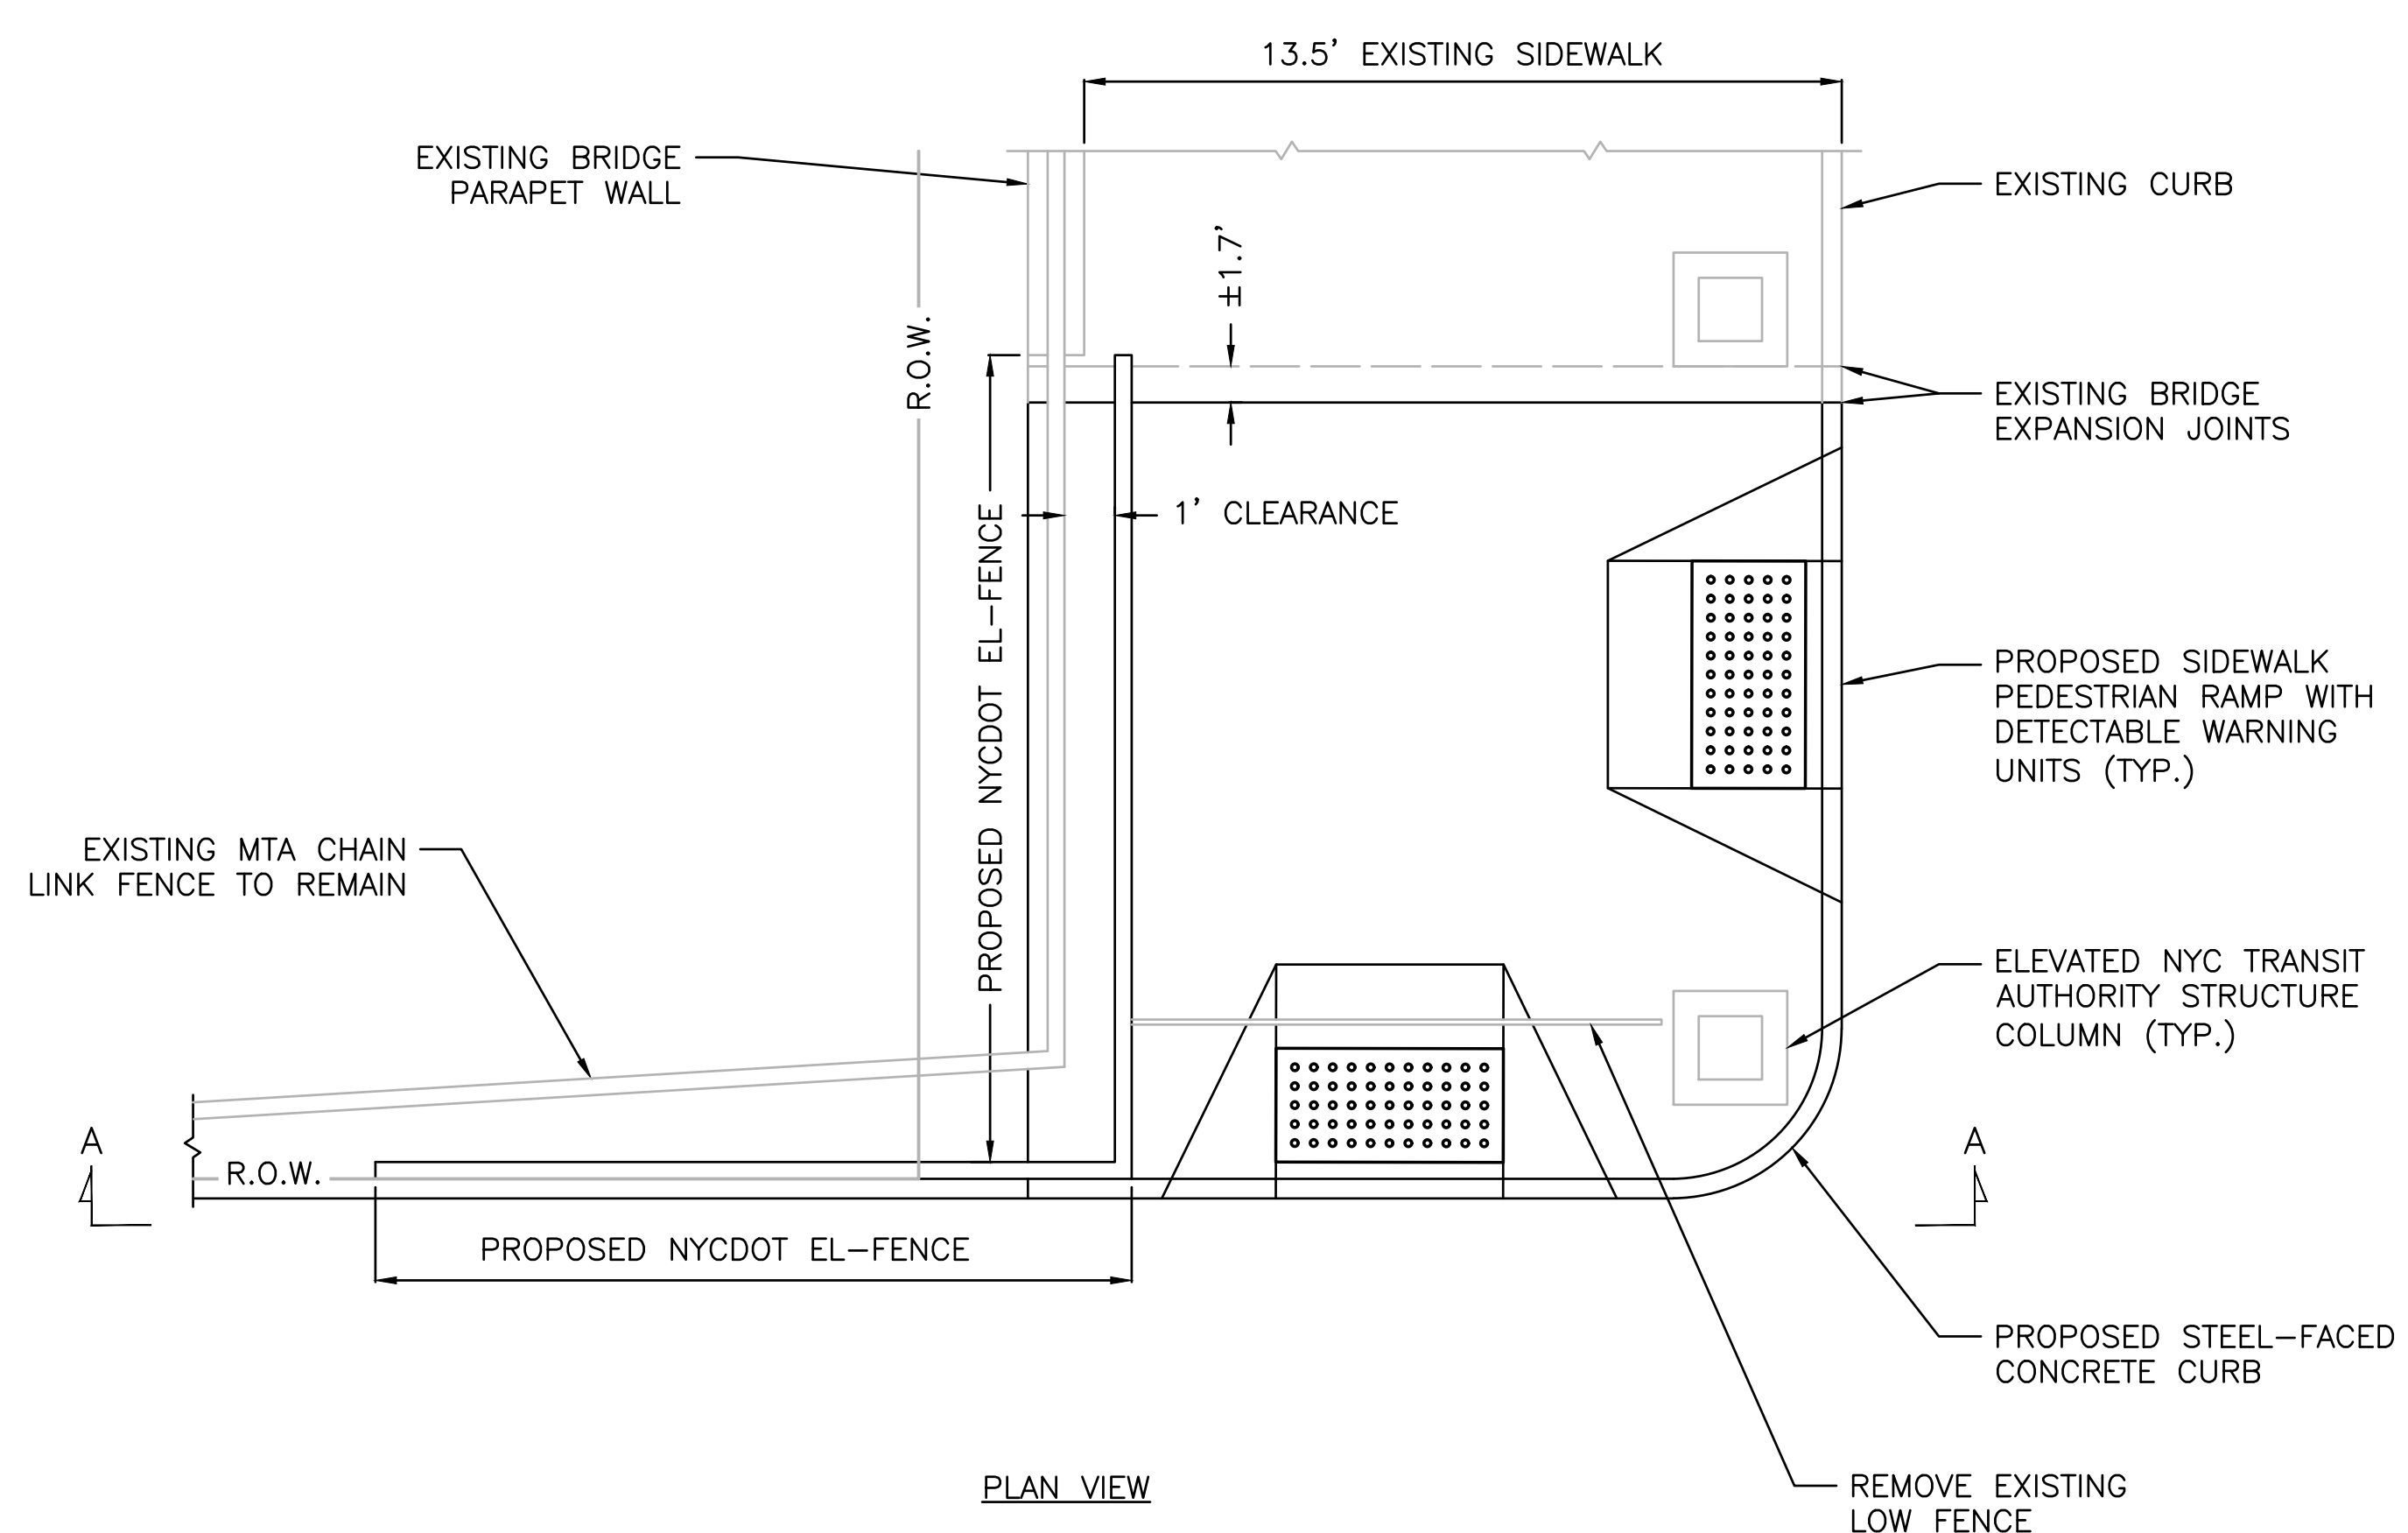

DETAIL #1
PROPOSED IMPROVEMENTS AT VAN SINDEREN AVENUE
AND SUTTER AVENUE INTERSECTION (SW CORNER)
SCALE: N.T.S.

NO.	DATE	DESCRIPTIONS REVISIONS						BY	APPR'	
VAN SINDEREN AVENUE STREETSCAPE IMPROVEMENTS BOROUGH OF BROOKLYN										
PROJECT ID: NDF-IBZ			DATE: 04/01/2019			SHEET 9 OF 22			97%	